THIS DOCUMENT IS PROPERTY OF KESLTD. & DUPLICATION OF ANY KIND IS PROHIBITED

GENERAL SPECIFICATIONS


GENERAL NOTES

1. All dimensions are shown in mm unless otherwise specified
2. Drawings are not to be scaled. Only figured dimensions to be used
3. Contractor must check and verify all dimensions on site before commencing of work
4. All slabs at ground level to be poured over 1000gauge polyethene sheet DPM on
5. 50 mm thick some dust on approved grade hardcore filling
6. All soil under the slabs and all around external foundation to be treated with anti-termites insecticide

ELECTRICAL INSTALLATION

1. All electrical installation works are to comply with the specified requirements and should be carried out by a qualified electrician providing requisite test certificates upon completion and installation.
2. Works should be carried out in accordance to approved code of practise


		KES LTD	PLEASE RETURN THE DOCUMENT WITH:	TITLE: SPECIFICATIONS	DRAWN BY: Stu.Eng.Brian Mumo	P.S
			NAME : STAMP:		APPROVED BY: Eng.Vincent..Jumba	A4
R1	25/2/2026		SIGNATURE :	PROJECT: HADU VOCATIONAL TRAINING CENTRE	DATE: 25/2/2026	Sh.No: 1
R0	19/2/2026		DATE :	CLIENT: ARCHSAN ASSOCIATES	QUOTE REF:Q001	Drg.No: 1

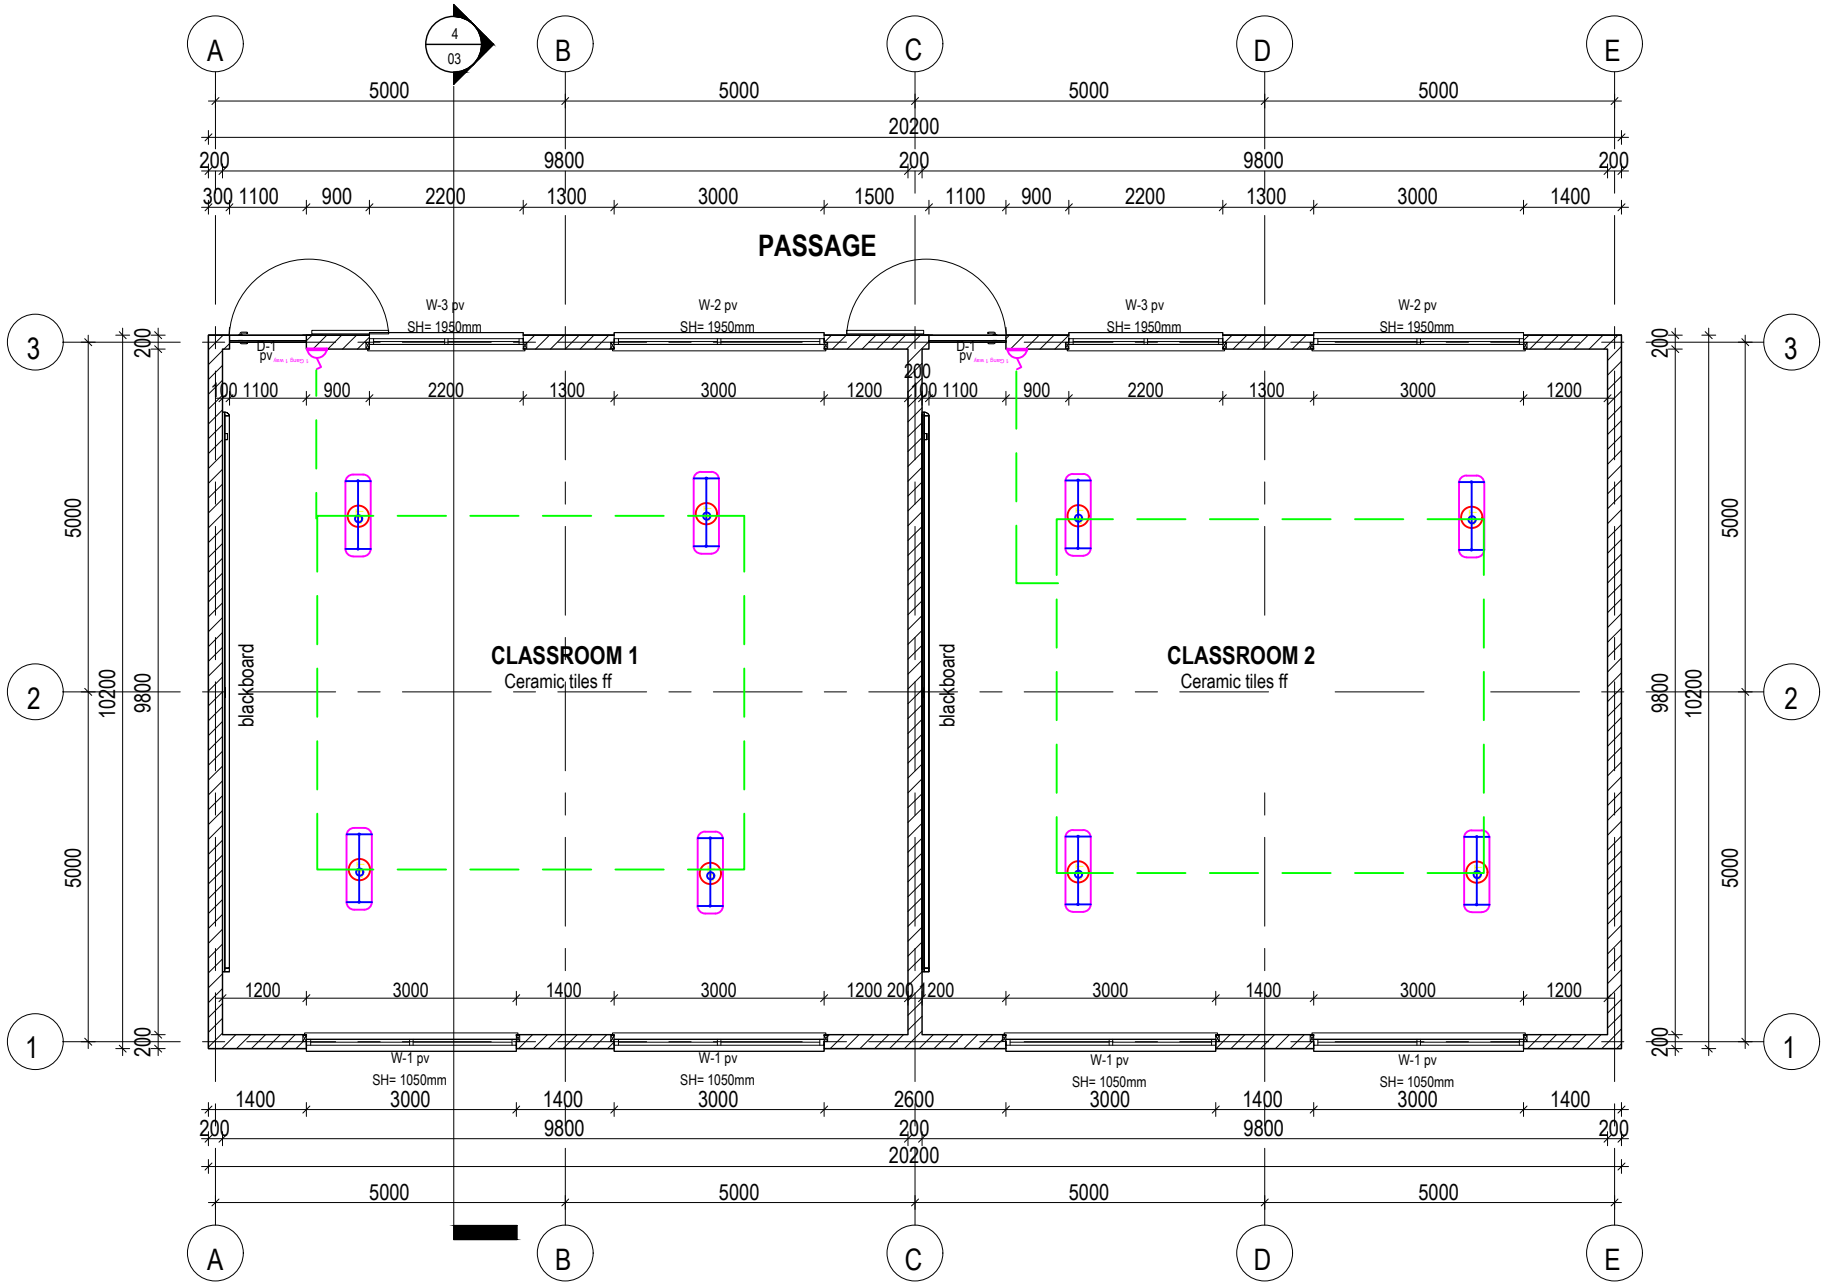

THIS DOCUMENT IS PROPERTY OF KESLTD. & DUPLICATION OF ANY KIND IS PROHIBITED

		PLEASE RETURN THE DOCUMENT WITH:	TITLE: BLOCK A LIGHTING DESIGN	DRAWN BY: Stu.Eng.Brian Mumo	P.S
		NAME : STAMP:		APPROVED BY: Eng.Vincent..Jumba	A4
R1	25/2/2026	SIGNATURE :	PROJECT: HADU VOCATIONAL TRAINING CENTRE	DATE: 25/2/2026	Sh.No: 1
R0	19/2/2026	DATE :	CLIENT: ARCHSAN ASSOCIATES	QUOTE REF:Q001	Drg.No: 1


THIS DOCUMENT IS PROPERTY OF KESLTD. & DUPLICATION OF ANY KIND IS PROHIBITED

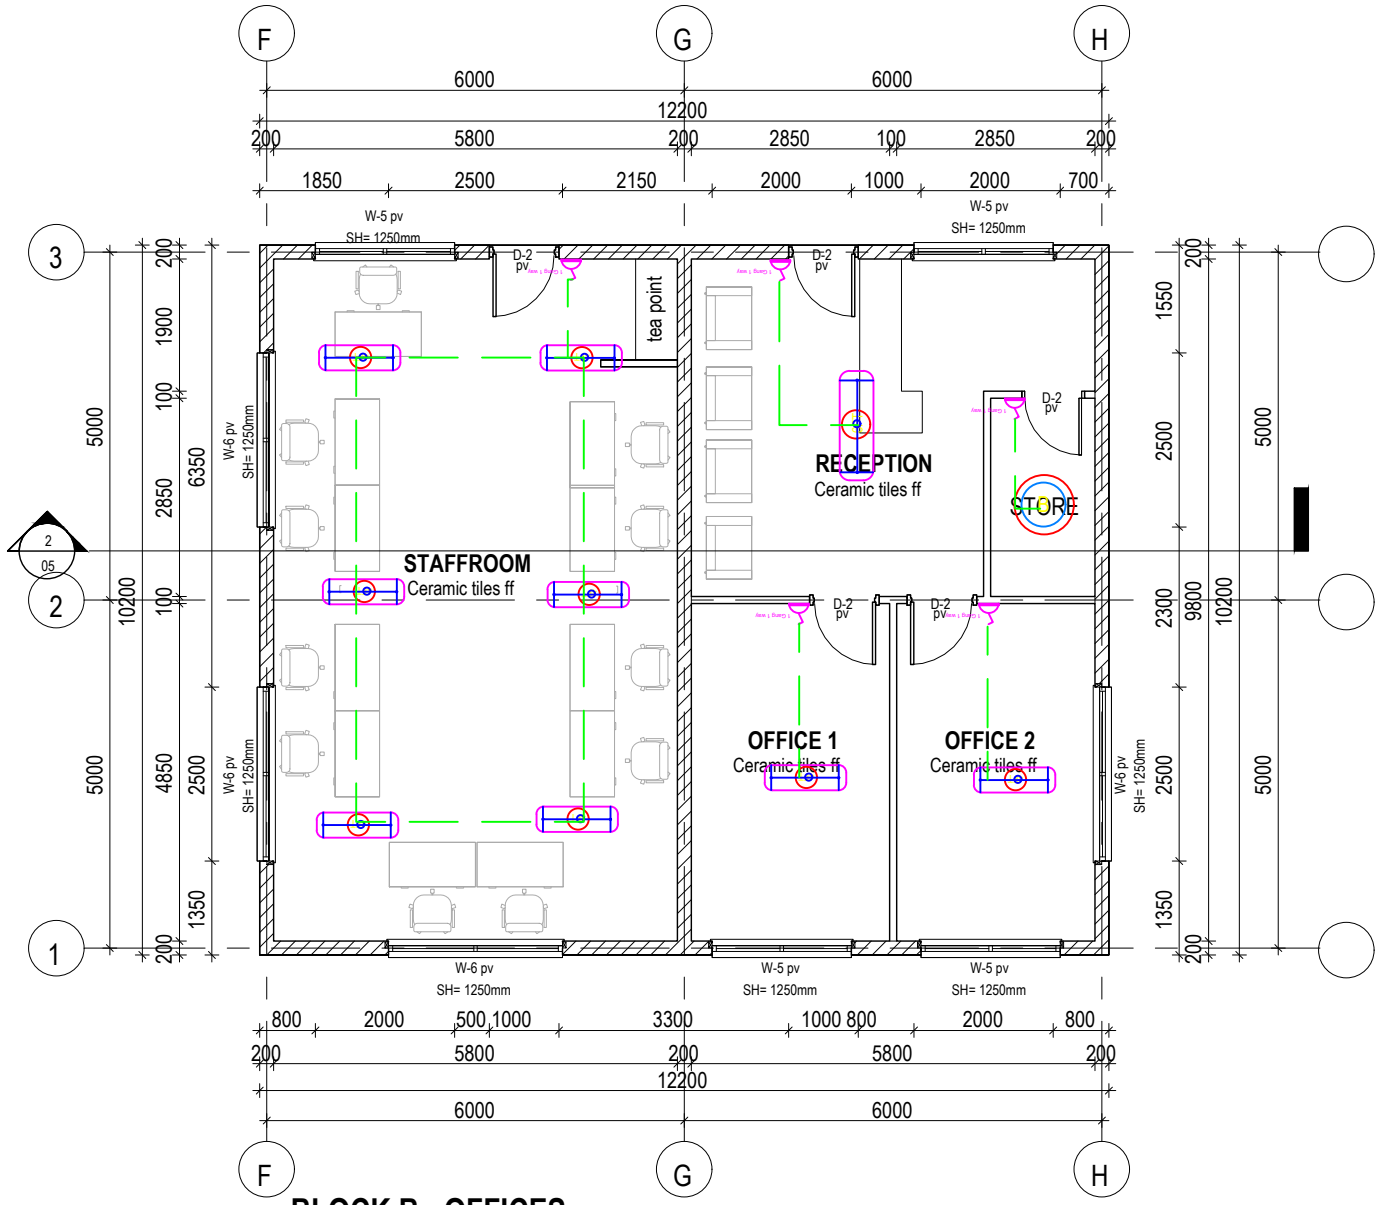

BLOCK B - OFFICES


		KES LTD Kamala Engineering Services	PLEASE RETURN THE DOCUMENT WITH:	TITLE: BLOCK B LIGHTING DESGN	DRAWN BY: Stu.Eng.Brian Mumo	P.S
			NAME : STAMP:		APPROVED BY: Eng.Vincent..Jumba	A4
R1	25/2/2026		SIGNATURE :	PROJECT: HADU VOCATIONAL TRAINING CENTRE	DATE: 25/2/2026	Sh.No: 1
R0	19/2/2026		DATE :	CLIENT: ARCHSAN ASSOCIATES	QUOTE REF:Q001	Drg.No: 1

THIS DOCUMENT IS PROPERTY OF KESLTD. & DUPLICATION OF ANY KIND IS PROHIBITED

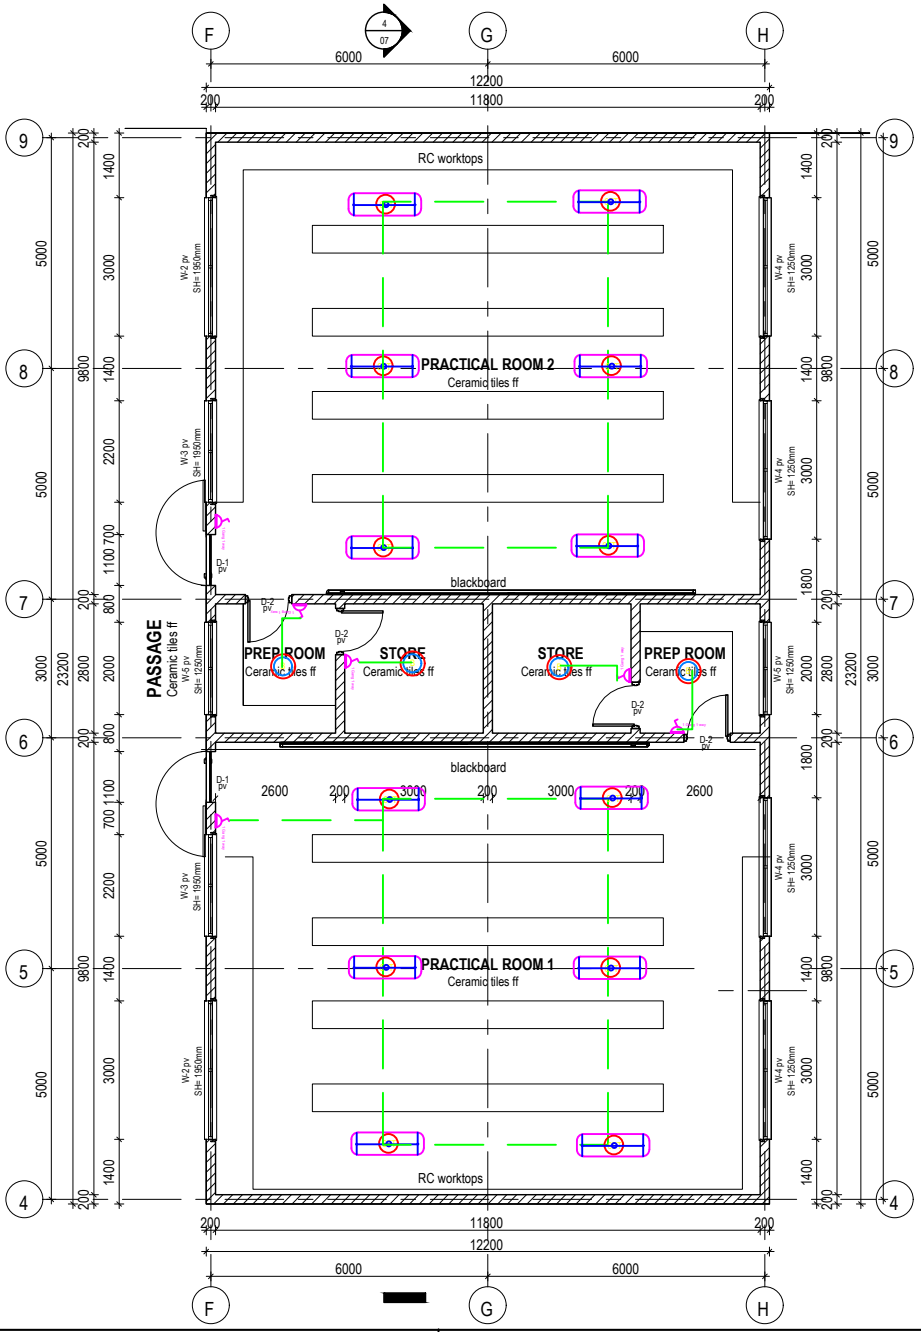

		PLEASE RETURN THE DOCUMENT WITH:	TITLE: BLOCK C LIGHTING DESIGN	DRAWN BY: Stu.Eng.Brian Mumo	P.S
		NAME : STAMP:		APPROVED BY: Eng.Vincent..Jumba	A4
R1	25/2/2026	SIGNATURE :	PROJECT: HADU VOCATIONAL TRAINING CENTRE	DATE: 25/2/2026	Sh.No: 1
R0	19/2/2026	DATE :	CLIENT: ARCHSAN ASSOCIATES	QUOTE REF:Q001	Drg.No: 1


THIS DOCUMENT IS PROPERTY OF KESLTD. & DUPLICATION OF ANY KIND IS PROHIBITED

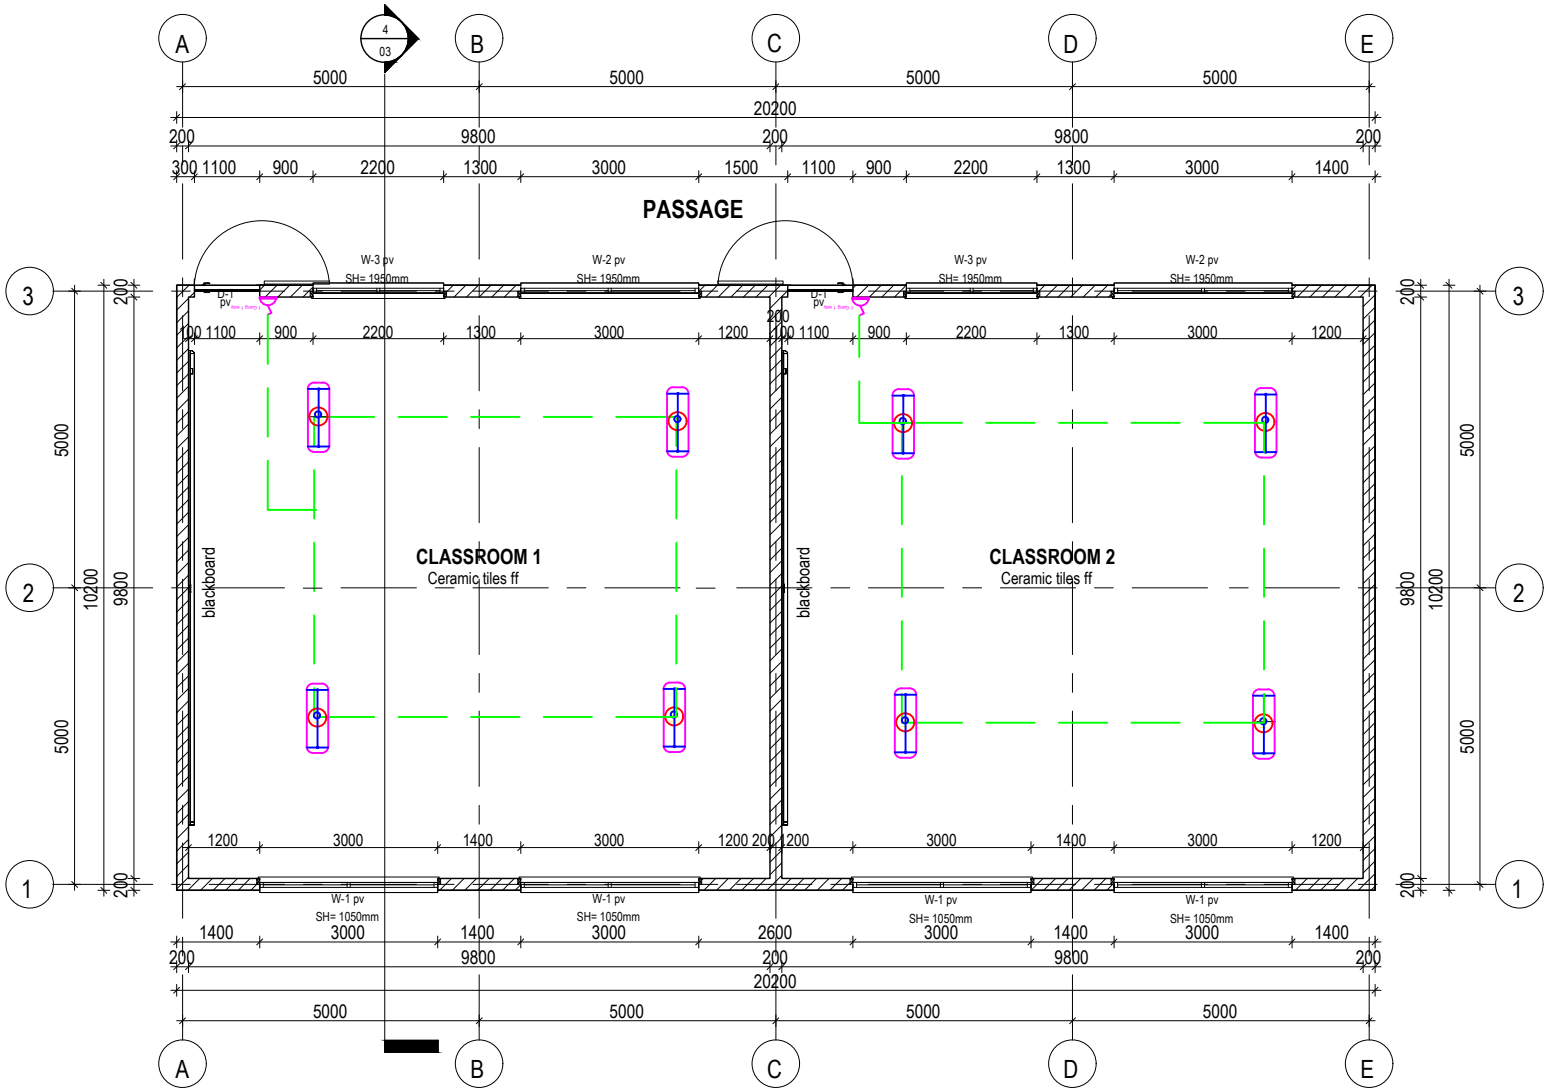

BLOCK D - CLASSROOMS

		KES LTD	PLEASE RETURN THE DOCUMENT WITH:	TITLE: BLOCK D LIGHTING DESIGN	DRAWN BY: Stu.Eng.Brian Mumo	P.S
			NAME : STAMP:		APPROVED BY: Eng.Vincent..Jumba	A4
R1	25/2/2026		SIGNATURE :	PROJECT: HADU VOCATIONAL TRAINING CENTRE	DATE: 25/2/2026	Sh.No: 1
R0	19/2/2026		DATE :	CLIENT: ARCHSAN ASSOCIATES	QUOTE REF:Q001	Drg.No: 1

THIS DOCUMENT IS PROPERTY OF KESLTD. & DUPLICATION OF ANY KIND IS PROHIBITED

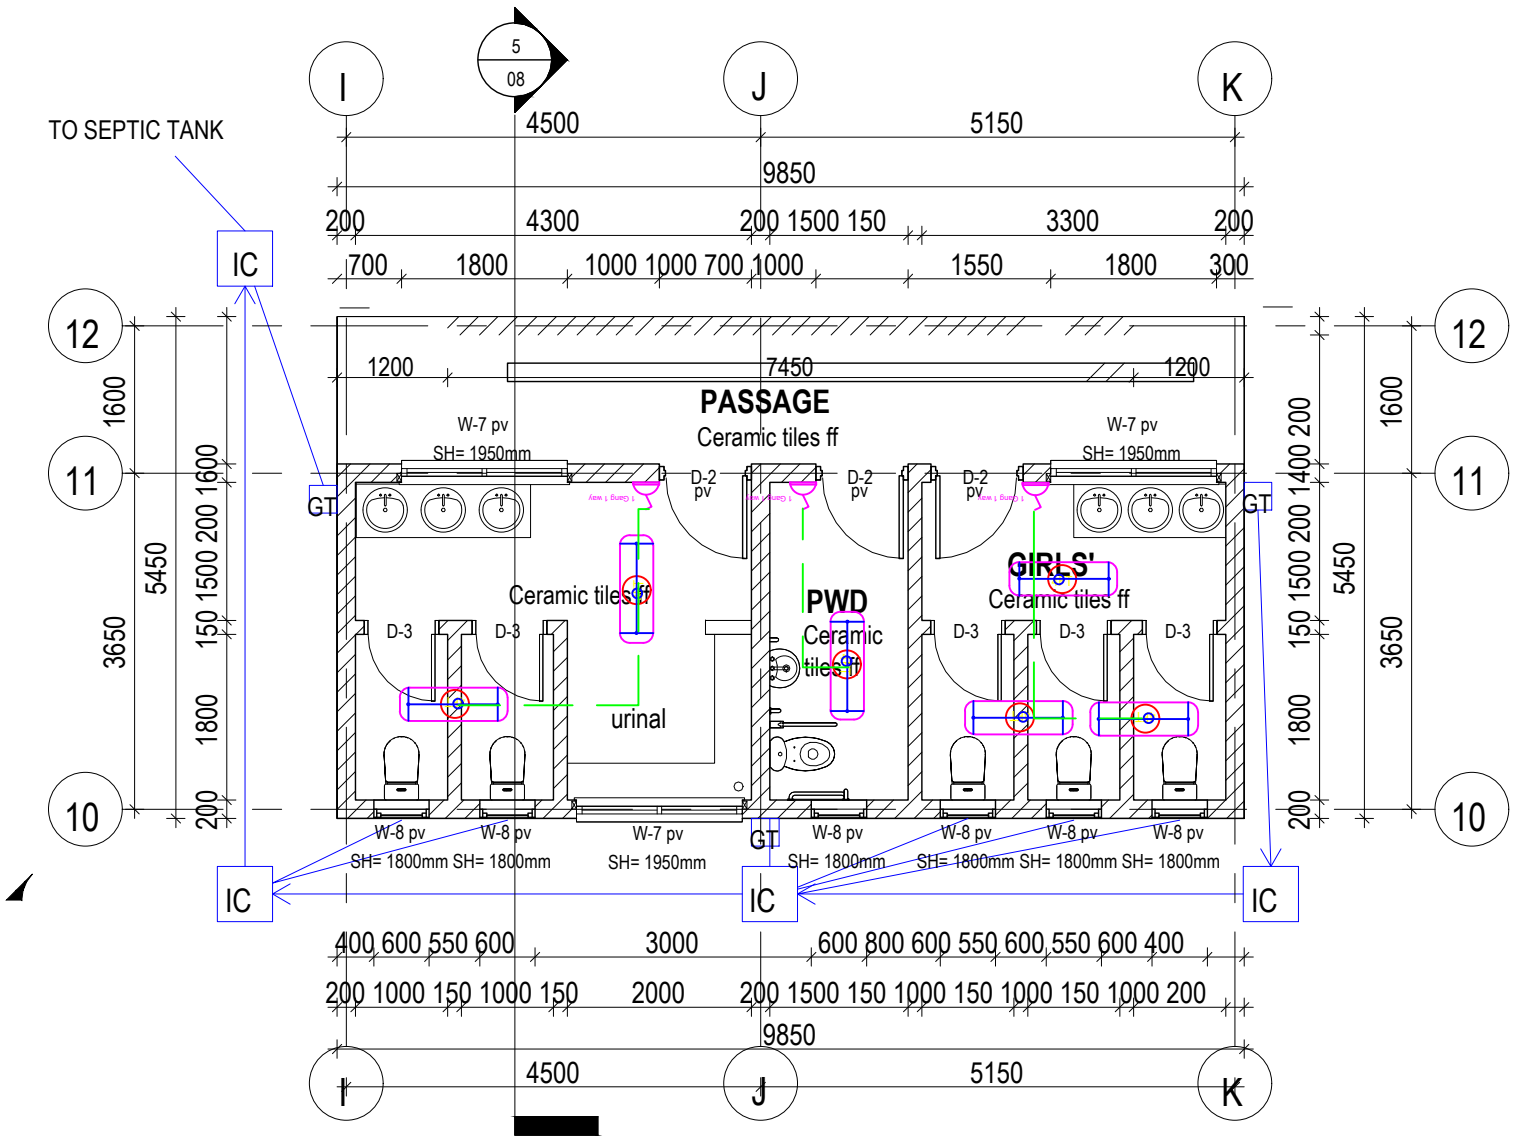

BLOCK E - ABLUTION BLOCK

FLOOR PLAN

		KES LTD	PLEASE RETURN THE DOCUMENT WITH:	TITLE: BLOCK E LIGHTING DESIGN	DRAWN BY: Stu.Eng.Brian Mumo	P.S
			NAME : STAMP:		APPROVED BY: Eng.Vincent..Jumba	A4
R1	25/2/2026		SIGNATURE :	PROJECT: HADU VOCATIONAL TRAINIG CENTRE	DATE: 25/2/2026	Sh.No: 1
R0	19/2/2026		DATE :	CLIENT: ARCHSAN ASSOCIATES	QUOTE REF:Q001	Drg.No: 1