

JUMBA BUILDWORKS

MECHANICAL + CONSTRUCTION

CONSTRUCTION DIVISION OF JUIMBA ENGINEERING SERVICES LIMITED
P.O BOX 8528-00300 , Nairobi
0722 266 799 /0727 924 355
Jes@jesltd.co.ke | jesltd.co.ke
BUILDING | CONSTRUCTION | ELECTRICAL | ICT

PROJECT :
12 HOUSE RENOVATIONS MUNAE ROAD

LOCATION
MUNAE ROAD

CLIENT :
GITHIAKA HOLDINGS LTD

DISCIPLINE:
MECHANICAL


DRAWING TITLE:
MECHANICAL FIXTURE SPECIFICATIONS

DRAWING STATUS :
APPROVAL

REV	DESCRIPTION	DATE
R0	INITIAL REVISION	16/10/2026

DRAWN BY:	Grad.Eng.Mumo Musyoki
CHECKED BY :	------
APPROVED BY:	Eng.Vincent Jumba
DATE:	16/10/2026
SCALE/SIZE:	1:100 @ A3
SHEET :	01 0F 01

DRAWING NO:	JBW-GTH-EL-[001]
SHEET :	01 OF 01
REVISION	R0

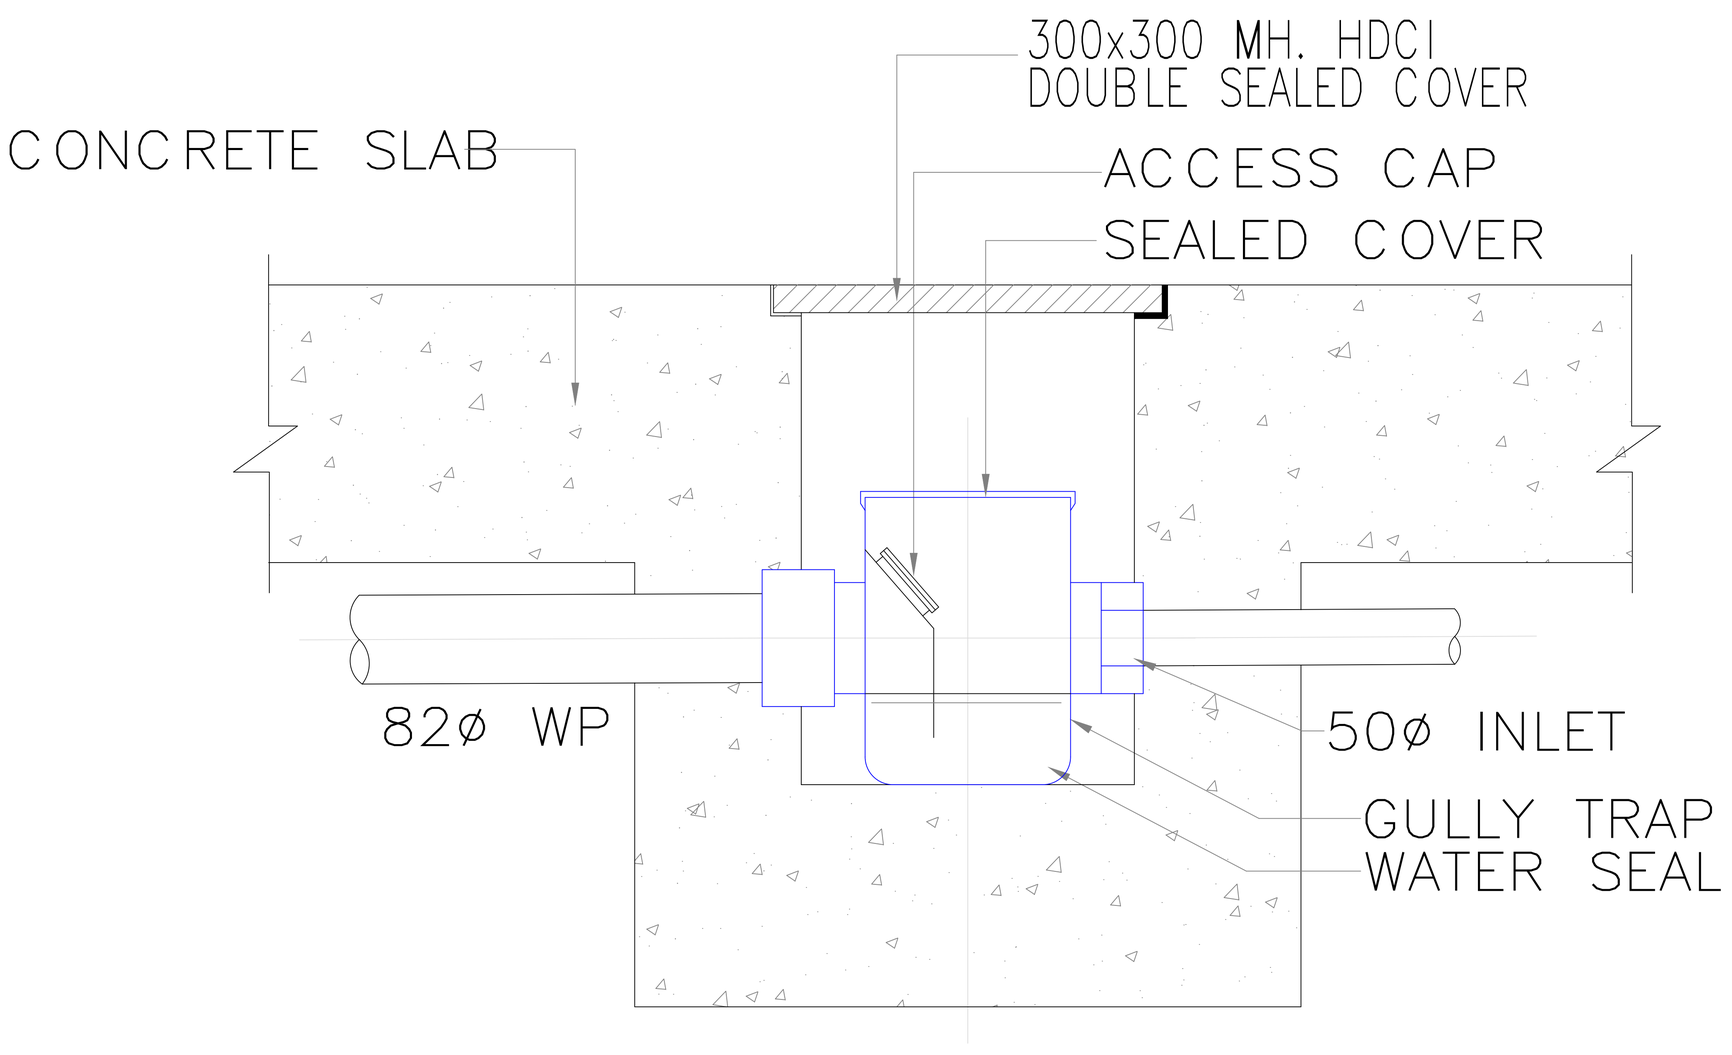

JUMBA BUILDWORKS

MECHANICAL + CONSTRUCTION

CONSTRUCTION DIVISION OF JUIMBA ENGINEERING SERVICES LIMITED
P.O BOX 8528-00300 , Nairobi
0722 266 799 /0727 924 355
Jes@jesltd.co.ke | jesltd.co.ke
BUILDING | CONSTRUCTION | ELECTRICAL | ICT

PROJECT :
12 HOUSE RENOVATIONS MUNAE ROAD

LOCATION
MUNAE ROAD

CLIENT :
GITHIAKA HOLDINGS LTD

DISCIPLINE:
MECHANICAL


DRAWING TITLE:
GULLY TRAP SPECIFICATIONS

DRAWING STATUS :
APPROVAL

REV	DESCRIPTION	DATE
R0	INITIAL REVISION	16/10/2026

DRAWN BY:	Grad.Eng.Mumo Musyoki
CHECKED BY :	------
APPROVED BY:	Eng.Vincent Jumba
DATE:	16/10/2026
SCALE/SIZE:	1:100 @ A3
SHEET :	01 0F 01

DRAWING NO:	JBW-GTH-EL-[001]
SHEET :	01 OF 01
REVISION	R0

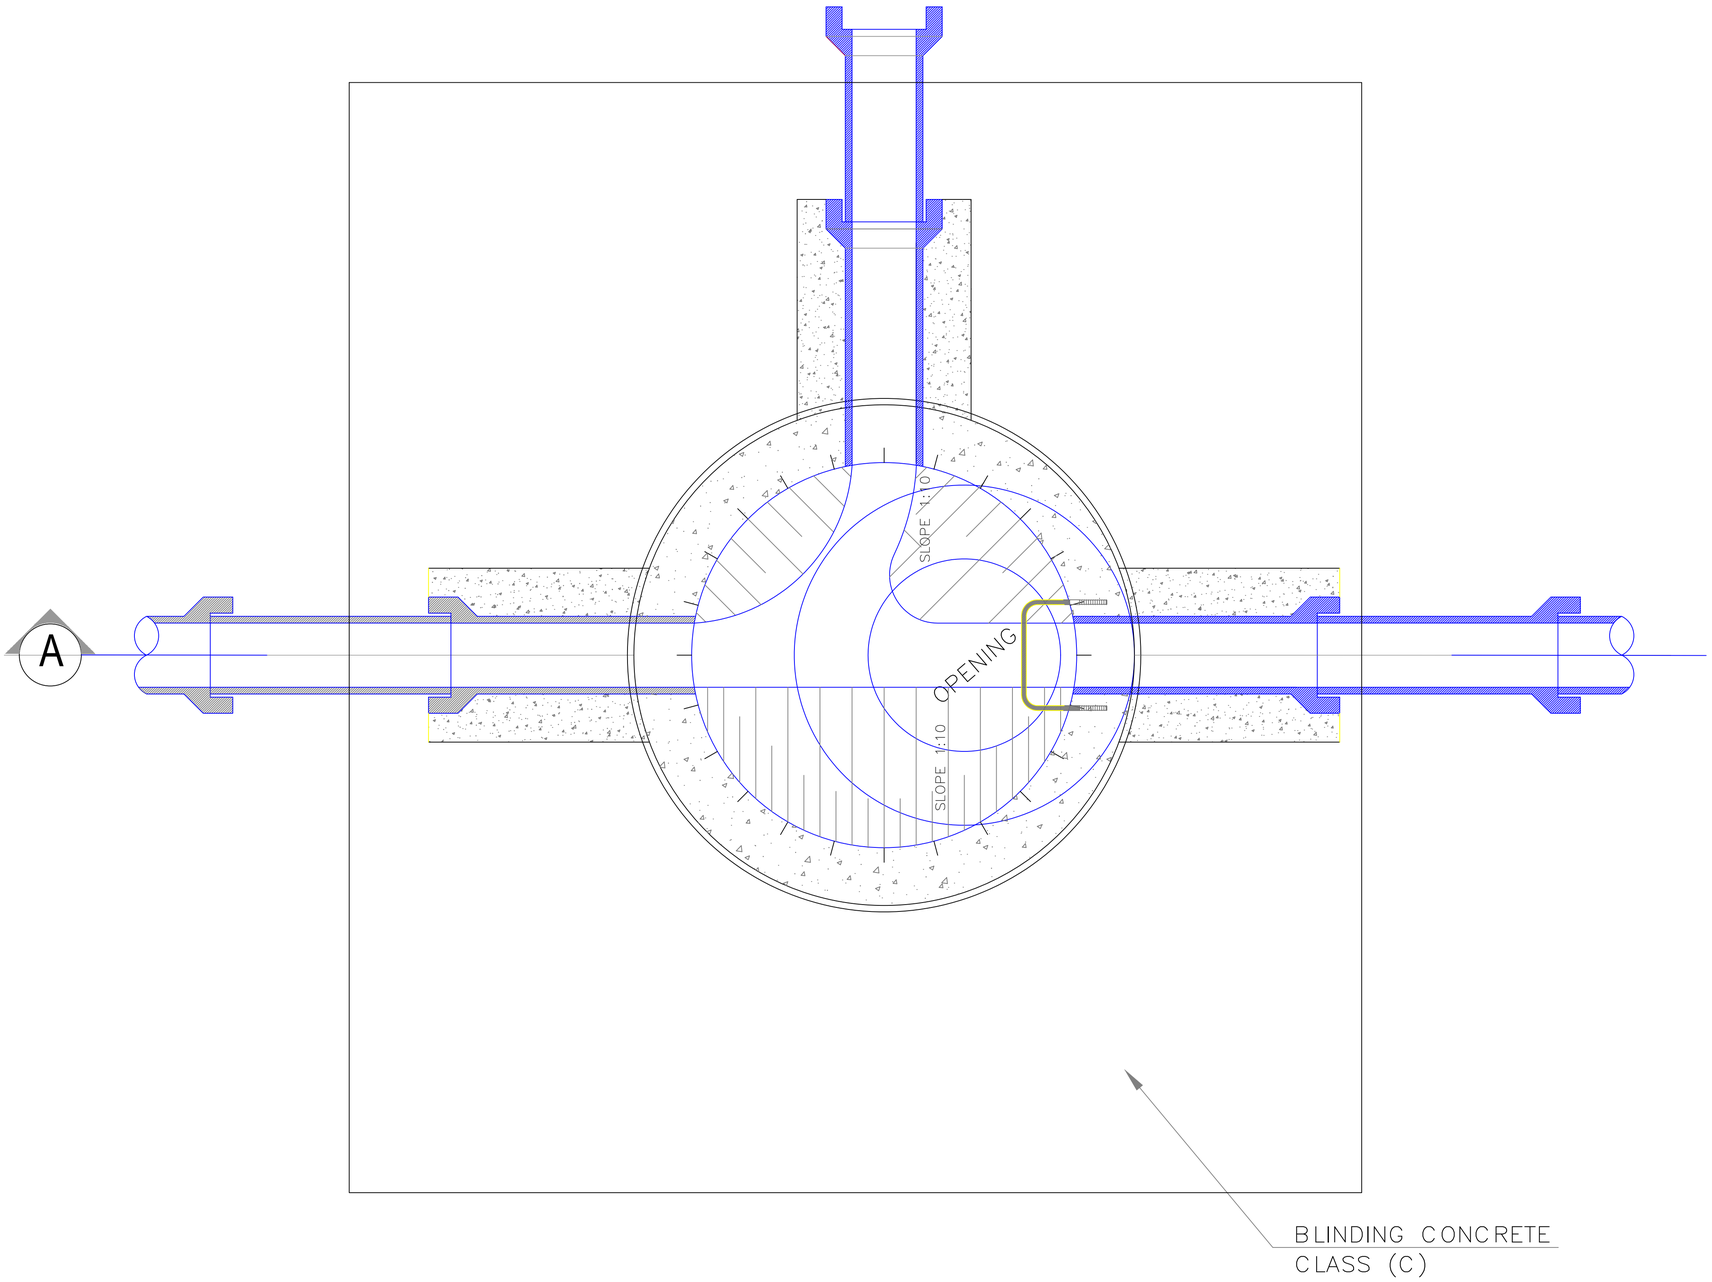

JUMBA BUILDWORKS

MECHANICAL + CONSTRUCTION

CONSTRUCTION DIVISION OF JUIMBA ENGINEERING SERVICES LIMITED
P.O BOX 8528-00300 , Nairobi
0722 266 799 /0727 924 355
Jes@jesltd.co.ke | jesltd.co.ke
BUILDING | CONSTRUCTION | ELECTRICAL | ICT

PROJECT :
12 HOUSE RENOVATIONS MUNAE ROAD

LOCATION
MUNAE ROAD

CLIENT :
GITHIAKA HOLDINGS LTD

DISCIPLINE:
MECHANICAL


DRAWING TITLE:
3 CHANNEL INSPECTION CHAMBER

DRAWING STATUS :
APPROVAL

REV	DESCRIPTION	DATE
R0	INITIAL REVISION	16/10/2026

DRAWN BY:	Grad.Eng.Mumo Musyoki
CHECKED BY :	------
APPROVED BY:	Eng.Vincent Jumba
DATE:	16/10/2026
SCALE/SIZE:	1:100 @ A3
SHEET :	01 0F 01

DRAWING NO:	JBW-GTH-EL-[001]
SHEET :	01 OF 01
REVISION	R0

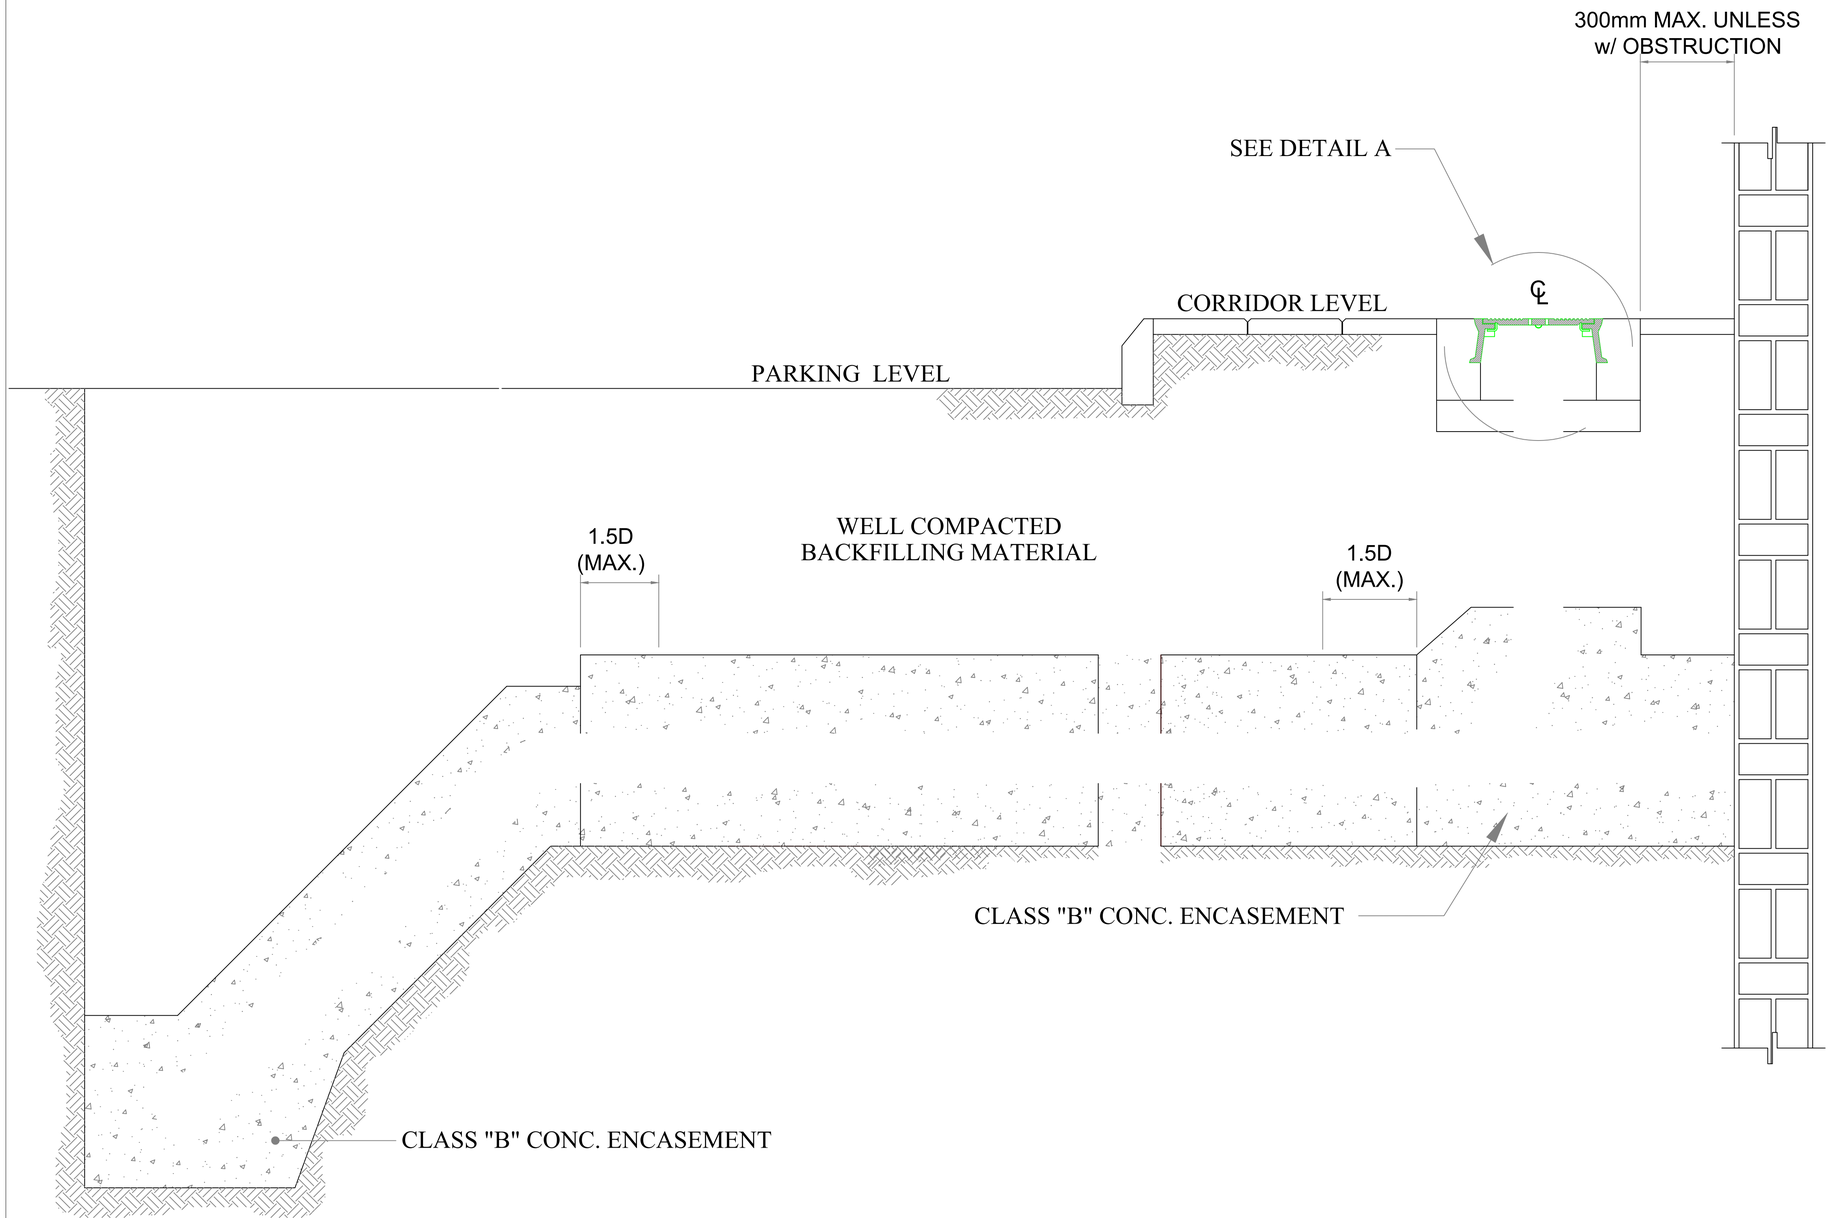

JUMBA BUILDWORKS

MECHANICAL + CONSTRUCTION

CONSTRUCTION DIVISION OF JUIMBA ENGINEERING SERVICES LIMITED
P.O BOX 8528-00300 , Nairobi
0722 266 799 /0727 924 355
Jes@jesltd.co.ke | jesltd.co.ke
BUILDING | CONSTRUCTION | ELECTRICAL | ICT

PROJECT :
12 HOUSE RENOVATIONS MUNAE ROAD

LOCATION
MUNAE ROAD

CLIENT :
GITHIAKA HOLDINGS LTD

DISCIPLINE:
MECHANICAL


DRAWING TITLE:
MANHOLE CHANNEL INTERCONNECTION

DRAWING STATUS :
APPROVAL

REV	DESCRIPTION	DATE
R0	INITIAL REVISION	16/10/2026

DRAWN BY:	Grad.Eng.Mumo Musyoki
CHECKED BY :	------
APPROVED BY:	Eng.Vincent Jumba
DATE:	16/10/2026
SCALE/SIZE:	1:100 @ A3
SHEET :	01 0F 01

DRAWING NO:	JBW-GTH-EL-[001]
SHEET :	01 OF 01
REVISION	R0

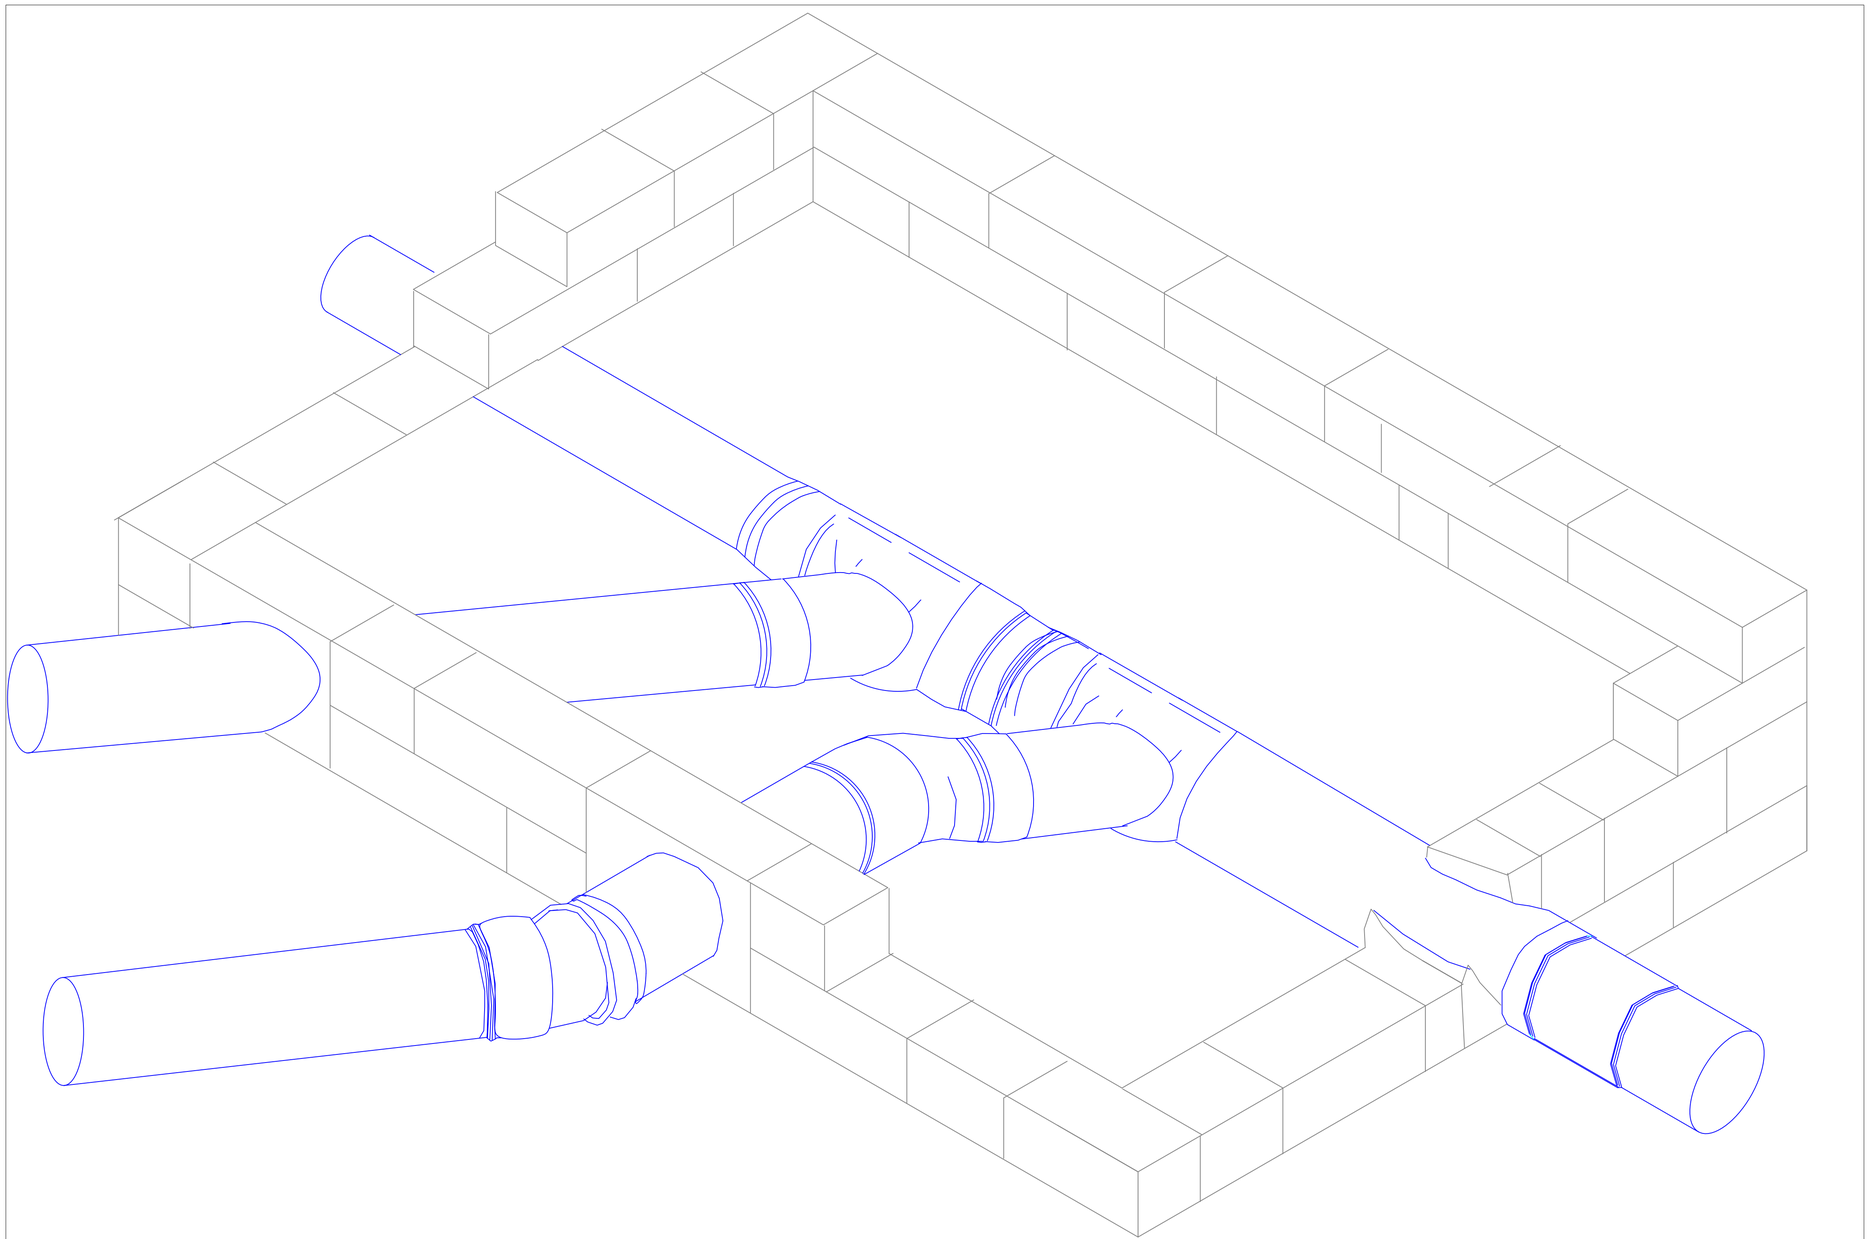

JUMBA BUILDWORKS

MECHANICAL + CONSTRUCTION

CONSTRUCTION DIVISION OF JUIMBA ENGINEERING SERVICES LIMITED
P.O BOX 8528-00300 , Nairobi
0722 266 799 /0727 924 355
Jes@jesltd.co.ke | jesltd.co.ke
BUILDING | CONSTRUCTION | ELECTRICAL | ICT

PROJECT :
12 HOUSE RENOVATIONS MUNAE ROAD

LOCATION
MUNAE ROAD

CLIENT :
GITHIAKA HOLDINGS LTD

DISCIPLINE:
MECHANICAL


DRAWING TITLE:
PVC PIPE ISOMETRIC INTERCONNECTION

DRAWING STATUS :
APPROVAL

REV	DESCRIPTION	DATE
R0	INITIAL REVISION	16/10/2026

DRAWN BY:	Grad.Eng.Mumo Musyoki
CHECKED BY :	------
APPROVED BY:	Eng.Vincent Jumba
DATE:	16/10/2026
SCALE/SIZE:	1:100 @ A3
SHEET :	01 0F 01

DRAWING NO:	JBW-GTH-EL-[001]
SHEET :	01 OF 01
REVISION	R0

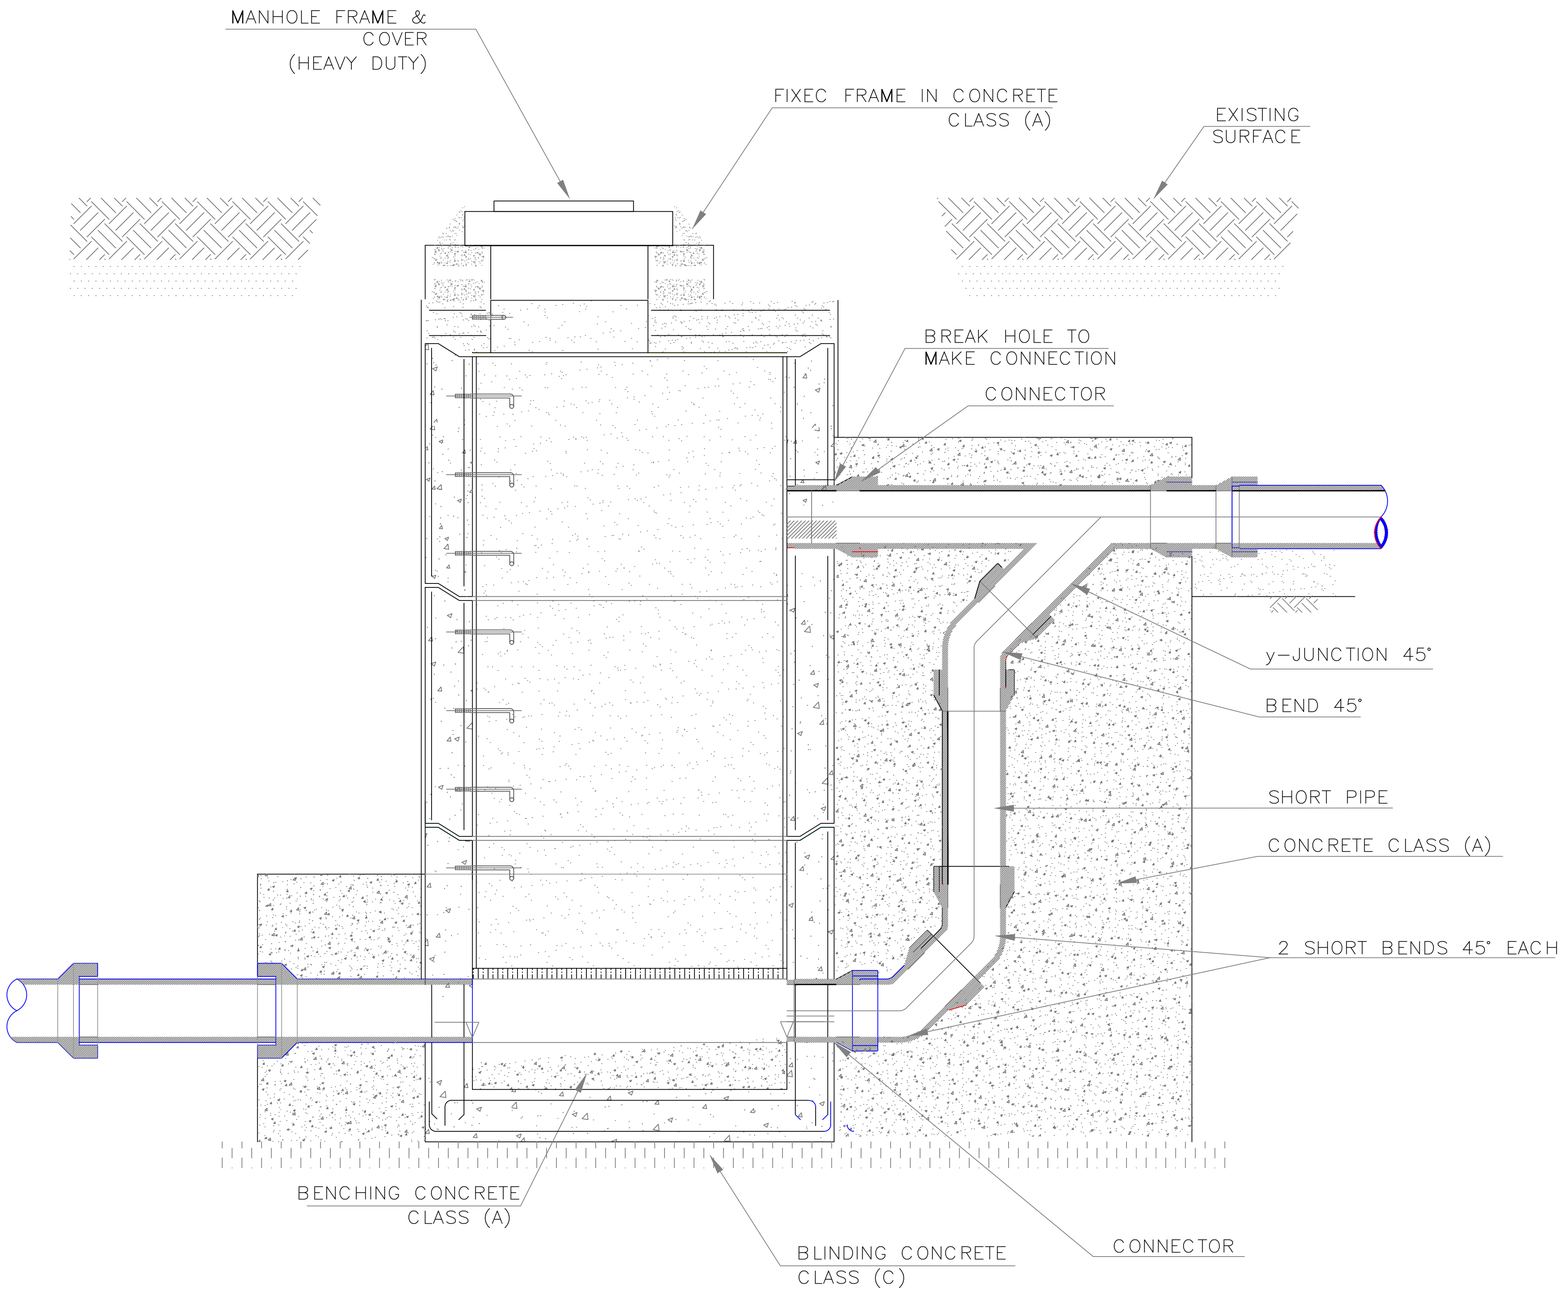

JUMBA BUILDWORKS

MECHANICAL + CONSTRUCTION

CONSTRUCTION DIVISION OF JUIMBA ENGINEERING SERVICES LIMITED
P.O BOX 8528-00300 , Nairobi
0722 266 799 /0727 924 355
Jes@jesltd.co.ke | jesltd.co.ke
BUILDING | CONSTRUCTION | ELECTRICAL | ICT

PROJECT :
12 HOUSE RENOVATIONS MUNAE ROAD

LOCATION
MUNAE ROAD

CLIENT :
GITHIAKA HOLDINGS LTD

DISCIPLINE:
MECHANICAL

DRAWING TITLE:
FINAL SERVICE MANHOLE

DRAWING STATUS :
APPROVAL

REV	DESCRIPTION	DATE
R0	INITIAL REVISION	16/10/2026

DRAWN BY:	Grad.Eng.Mumo Musyoki
CHECKED BY :	------
APPROVED BY:	Eng.Vincent Jumba
DATE:	16/10/2026
SCALE/SIZE:	1:100 @ A3
SHEET :	01 0F 01

DRAWING NO:	JBW-GTH-EL-[001]
SHEET :	01 OF 01
REVISION	R0