

THIS DOCUMENT IS PROPERTY OF KESLTD. & DUPLICATION OF ANY KIND IS PROHIBITED

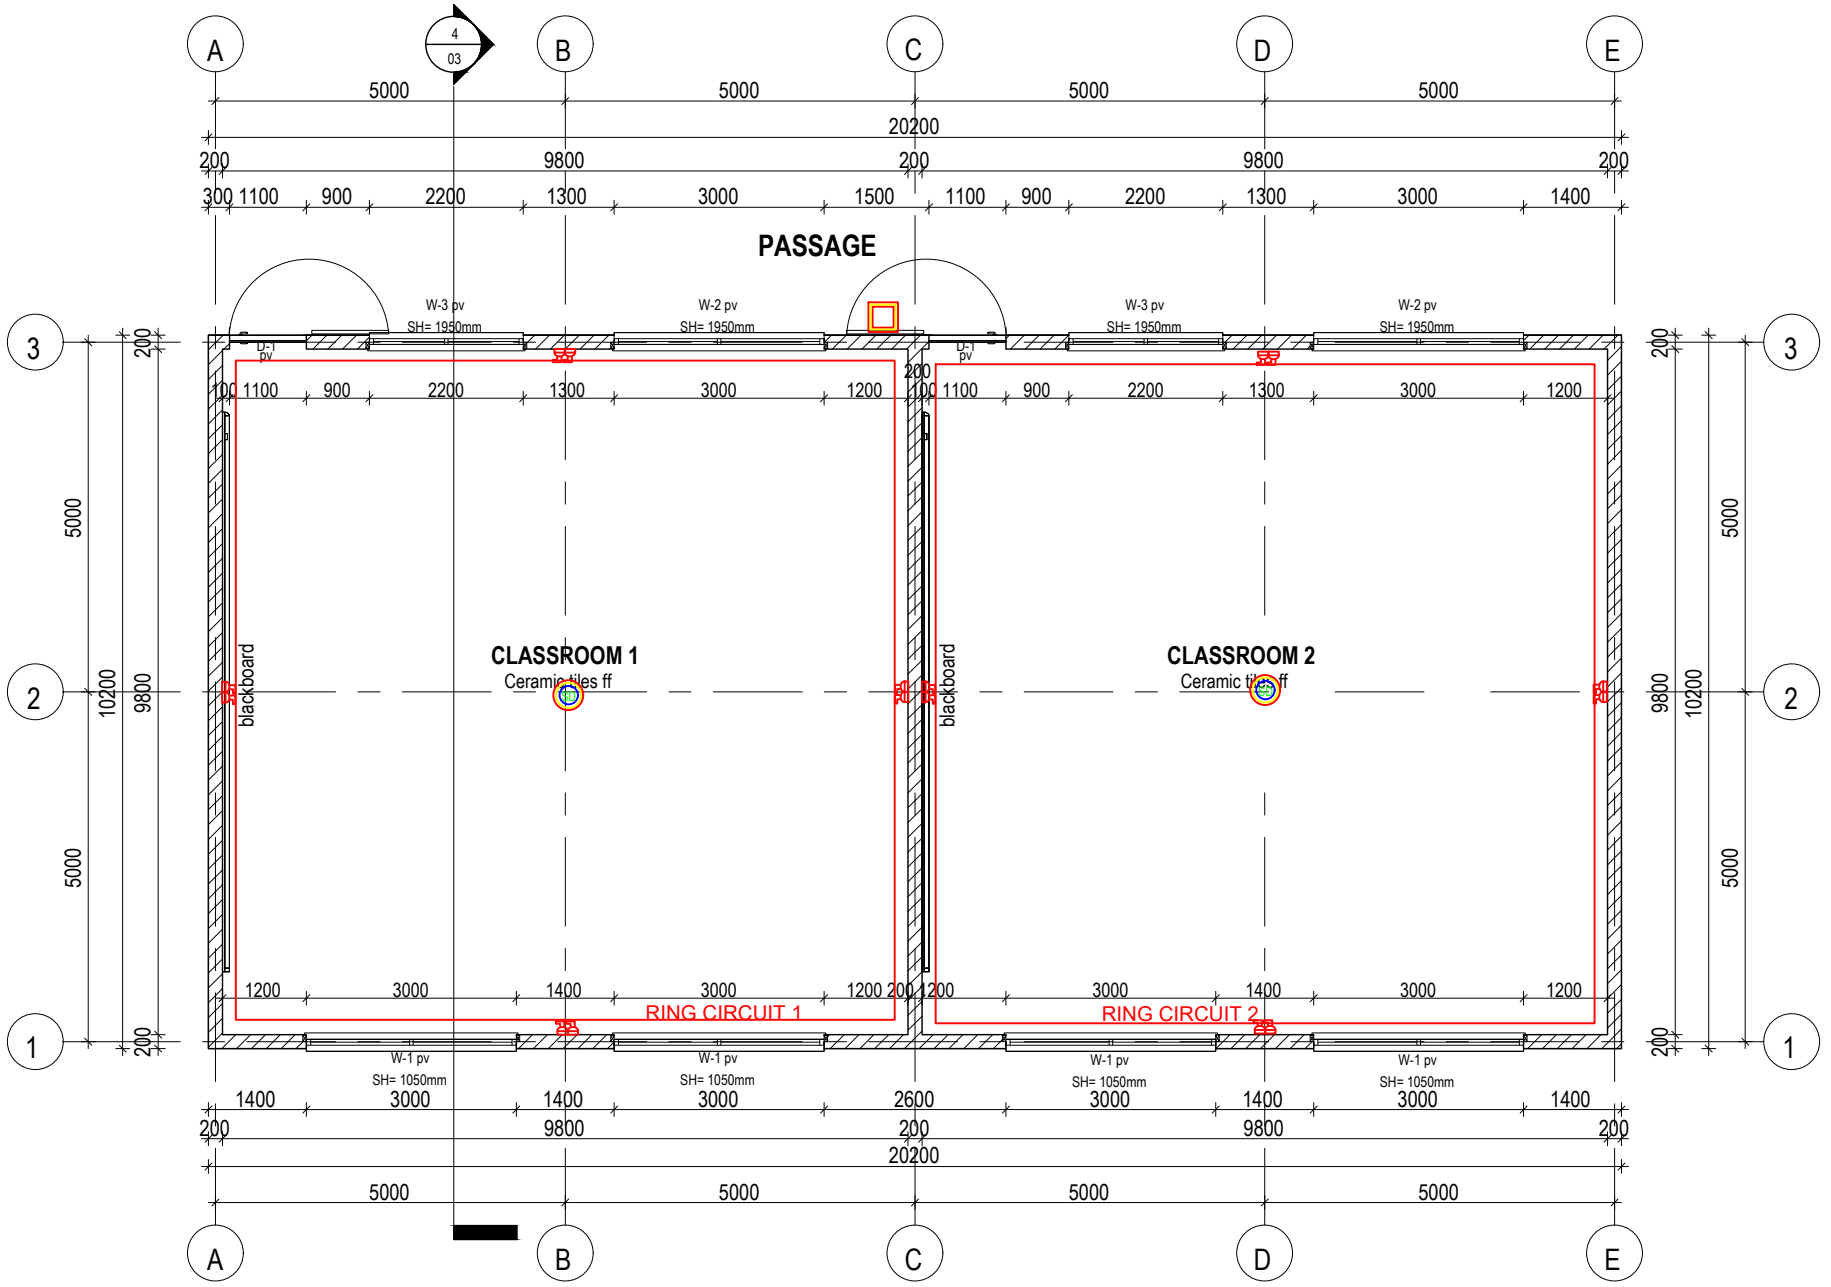

		PLEASE RETURN THE DOCUMENT WITH:	TITLE: BLOCK A LIGHTING DESIGN	DRAWN BY: Stu.Eng.Brian Mumo	P.S
		NAME : STAMP:		APPROVED BY: Eng.Vincent..Jumba	A4
R1	25/2/2026	SIGNATURE :	PROJECT: HADU VOCATIONAL TRAINING CENTRE	DATE: 25/2/2026	Sh.No: 1
R0	19/2/2026	DATE :	CLIENT: ARCHSAN ASSOCIATES	QUOTE REF:Q001	Drg.No: 1


THIS DOCUMENT IS PROPERTY OF KESLTD. & DUPLICATION OF ANY KIND IS PROHIBITED

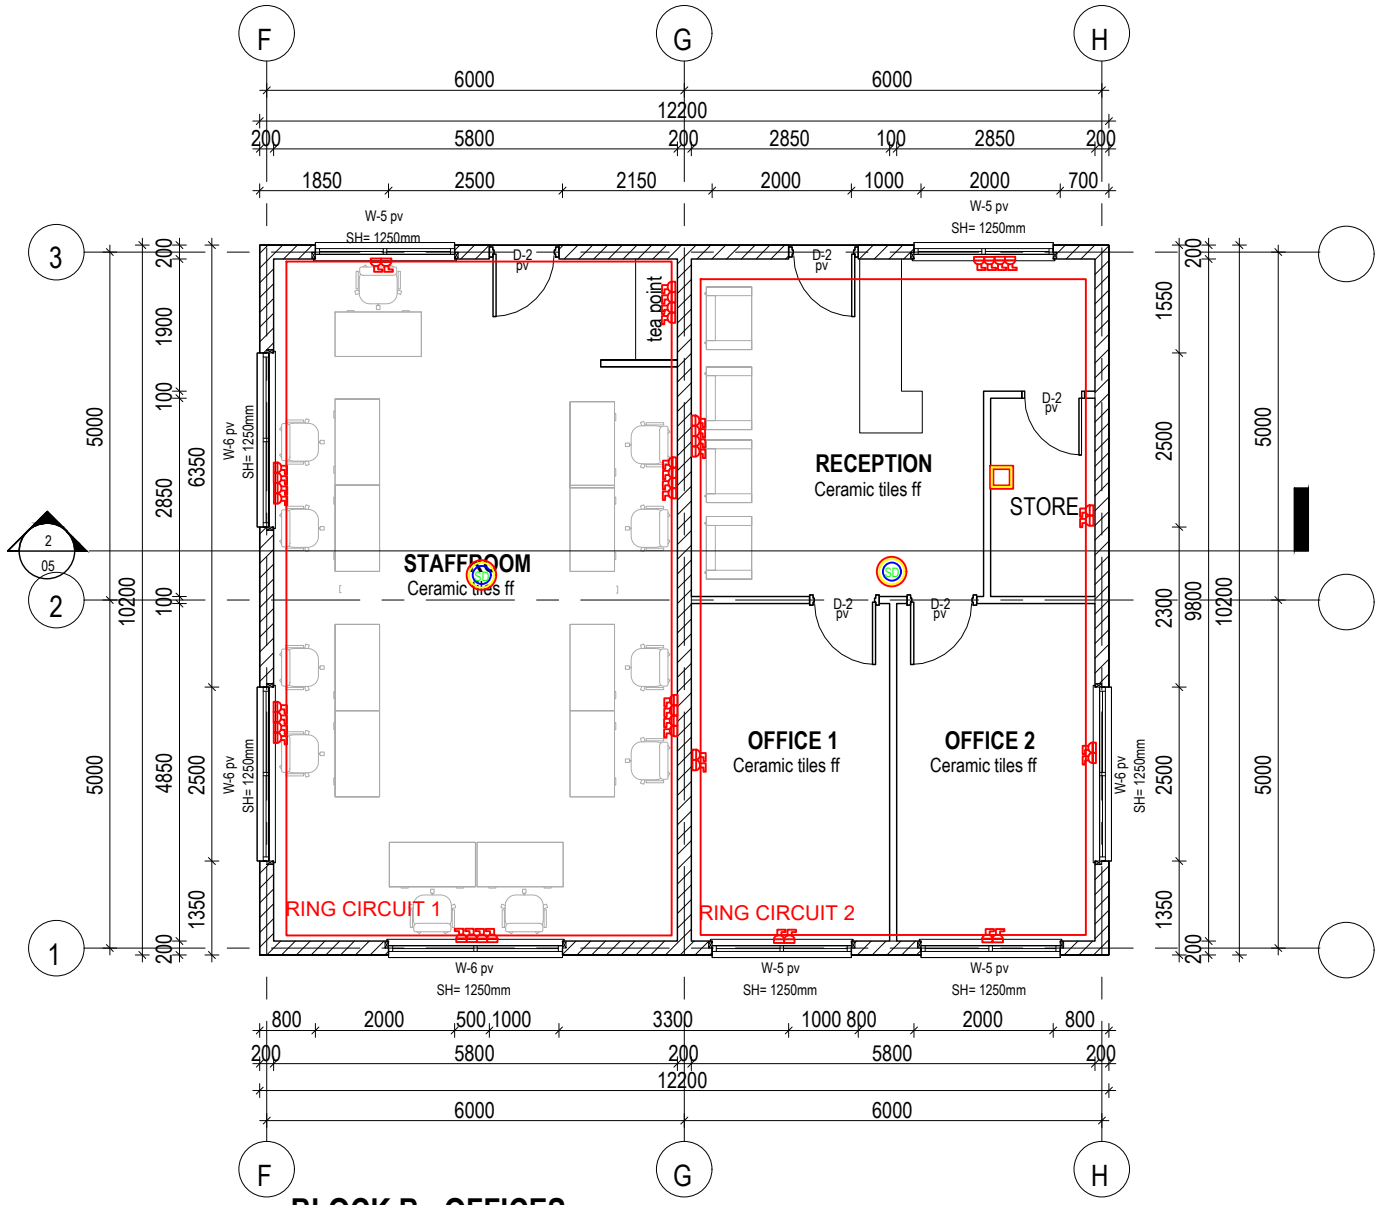

BLOCK B - OFFICES


		PLEASE RETURN THE DOCUMENT WITH:	TITLE: BLOCK B LIGHTING DESGN	DRAWN BY: Stu.Eng.Brian Mumo	P.S	
		NAME :	STAMP:	APPROVED BY: Eng.Vincent..Jumba	A4	
R1	25/2/2026	SIGNATURE :	PROJECT: HADU VOCATIONAL TRAINING CENTRE	DATE: 25/2/2026	Sh.No: 1	
R0	19/2/2026	DATE :	CLIENT: ARCHSAN ASSOCIATES	QUOTE REF:Q001	Drg.No: 1	

THIS DOCUMENT IS PROPERTY OF KESLTD. & DUPLICATION OF ANY KIND IS PROHIBITED

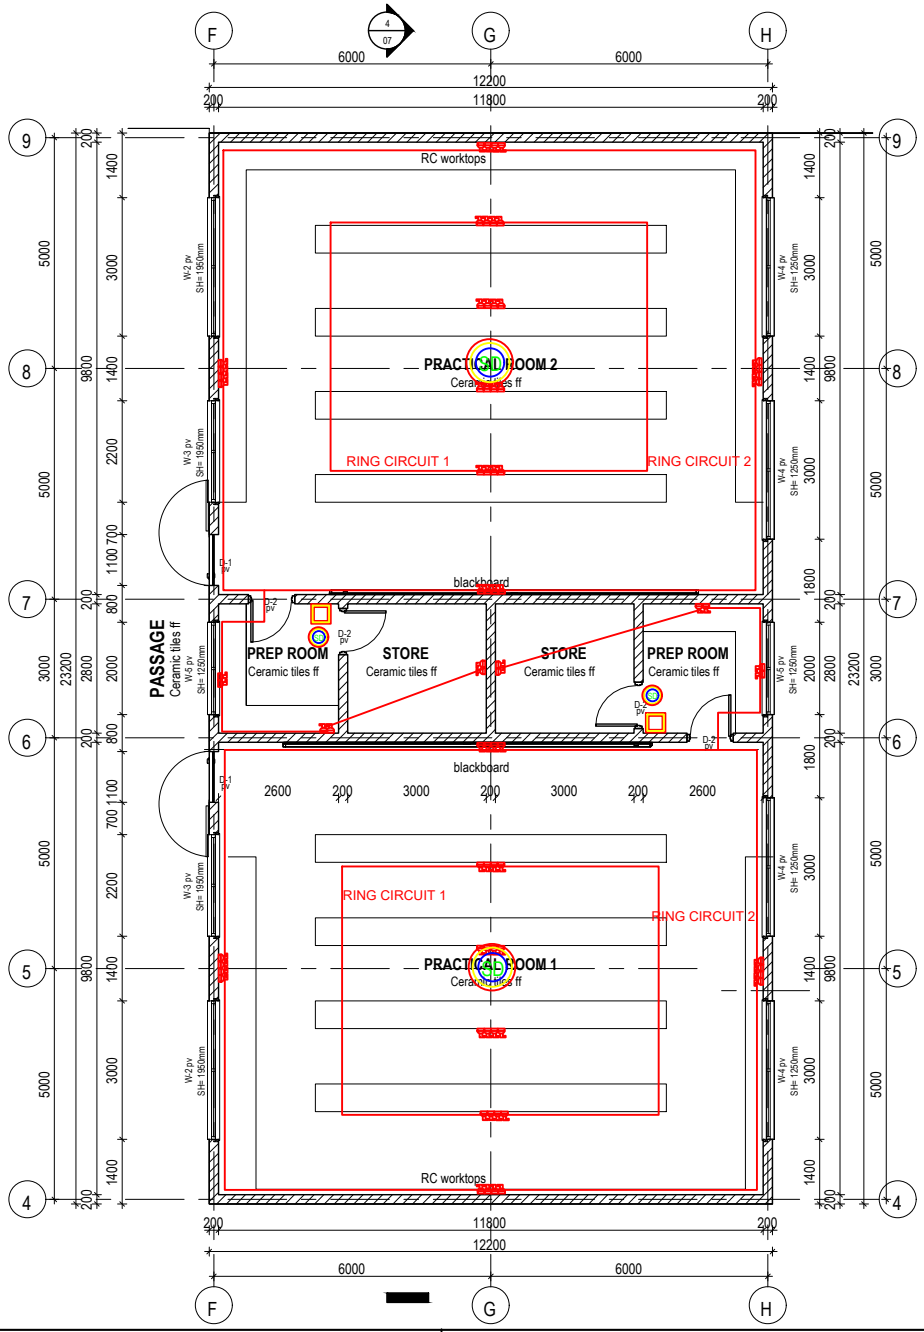

		PLEASE RETURN THE DOCUMENT WITH:	TITLE: BLOCK C LIGHTING DESIGN	DRAWN BY: Stu.Eng.Brian Mumo	P.S
		NAME : STAMP:		APPROVED BY: Eng.Vincent..Jumba	A4
R1	25/2/2026	SIGNATURE :	PROJECT: HADU VOCATIONAL TRAINING CENTRE	DATE: 25/2/2026	Sh.No: 1
R0	19/2/2026	DATE :	CLIENT: ARCHSAN ASSOCIATES	QUOTE REF:Q001	Drg.No: 1


THIS DOCUMENT IS PROPERTY OF KESLTD. & DUPLICATION OF ANY KIND IS PROHIBITED

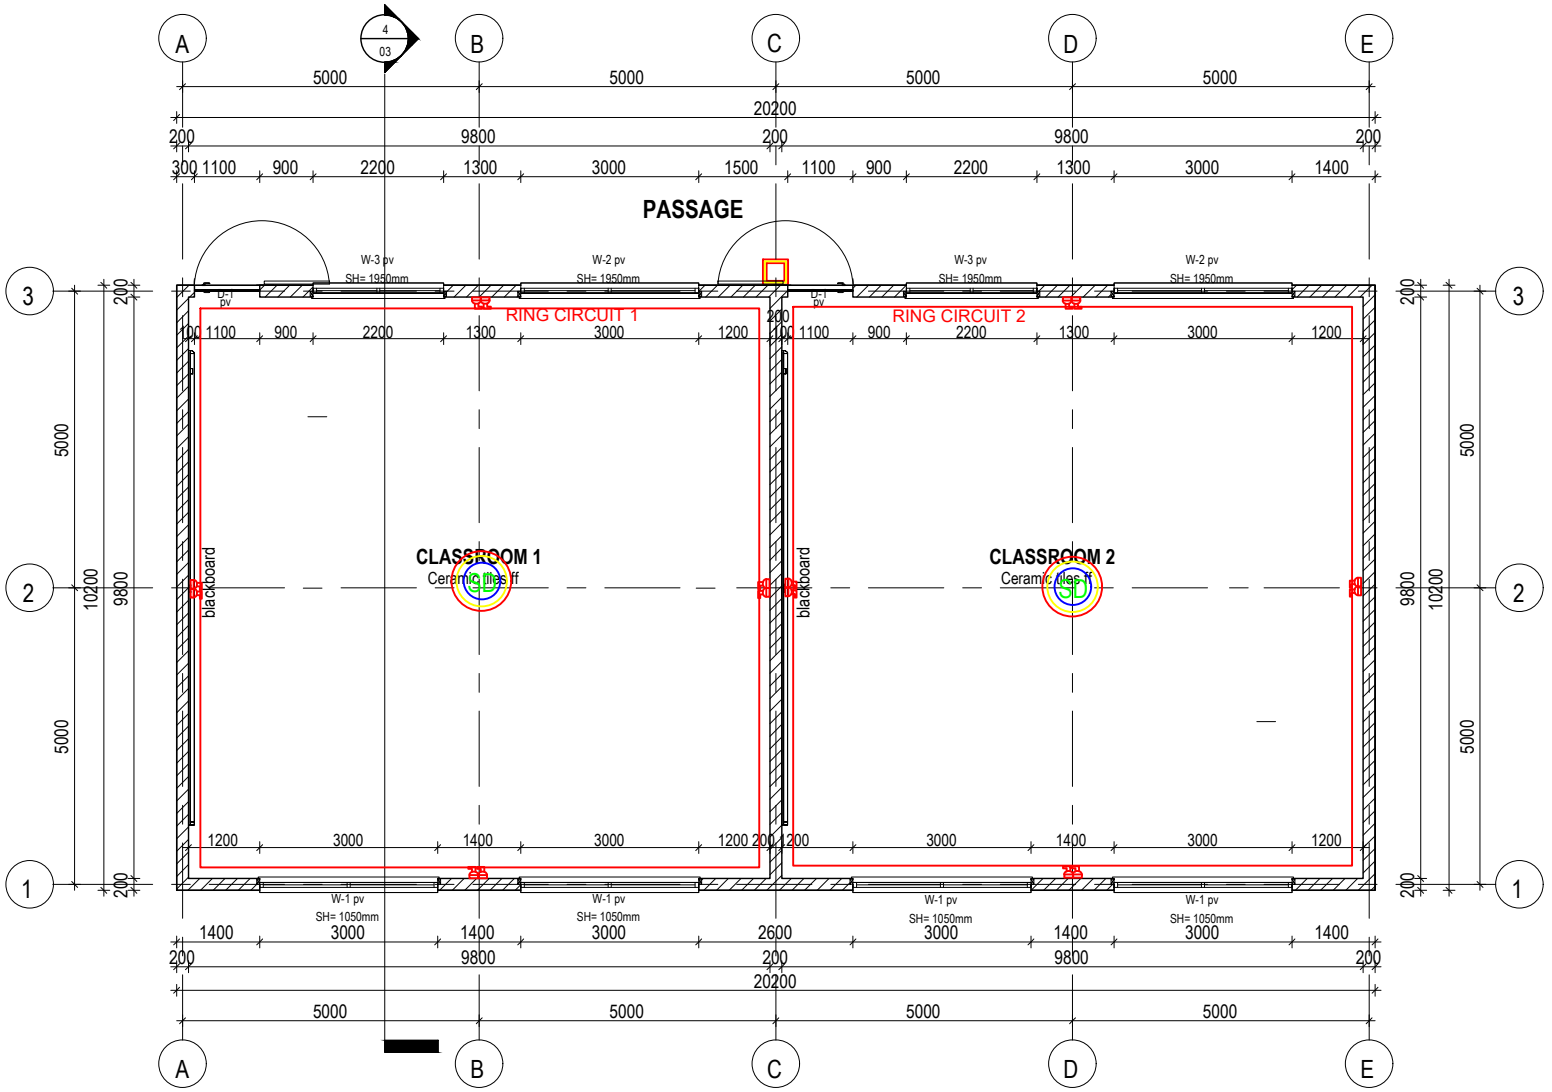

BLOCK D - CLASSROOMS

		PLEASE RETURN THE DOCUMENT WITH:		TITLE: BLOCK D LIGHTING DESIGN	DRAWN BY: Stu.Eng.Brian Mumo	P.S
		NAME :	STAMP:		APPROVED BY: Eng.Vincent..Jumba	A4
R1	25/2/2026	SIGNATURE :		PROJECT: HADU VOCATIONAL TRAINING CENTRE	DATE: 25/2/2026	Sh.No: 1
R0	19/2/2026	DATE :		CLIENT: ARCHSAN ASSOCIATES	QUOTE REF:Q001	Drg.No: 1

THIS DOCUMENT IS PROPERTY OF KESLTD. & DUPLICATION OF ANY KIND IS PROHIBITED

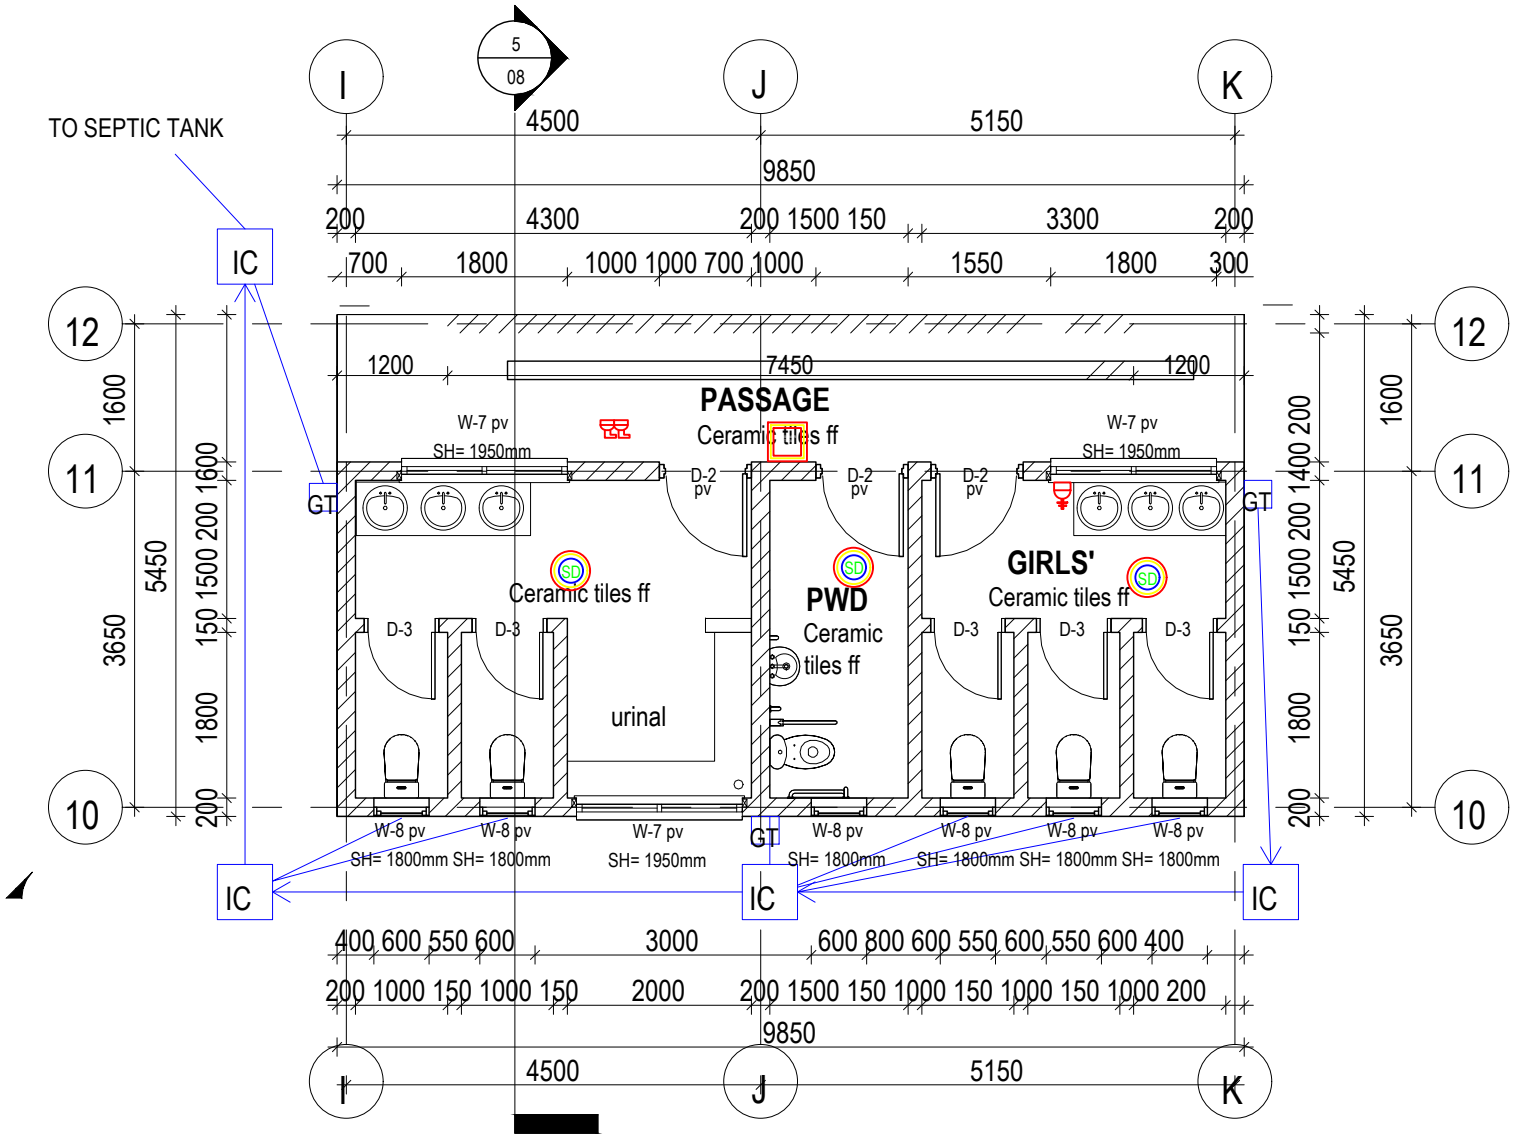


BLOCK E - ABLUTION BLOCK

FLOOR PLAN


		KES LTD	PLEASE RETURN THE DOCUMENT WITH:	TITLE: BLOCK E LIGHTING DESIGN	DRAWN BY: Stu.Eng.Brian Mumo	P.S
			NAME : STAMP:		APPROVED BY: Eng.Vincent..Jumba	A4
R1	25/2/2026		SIGNATURE :	PROJECT: HADU VOCATIONAL TRAINIG CENTRE	DATE: 25/2/2026	Sh.No: 1
R0	19/2/2026		DATE :	CLIENT: ARCHSAN ASSOCIATES	QUOTE REF:Q001	Drg.No: 1

THIS DOCUMENT IS PROPERTY OF KESLTD. & DUPLICATION OF ANY KIND IS PROHIBITED

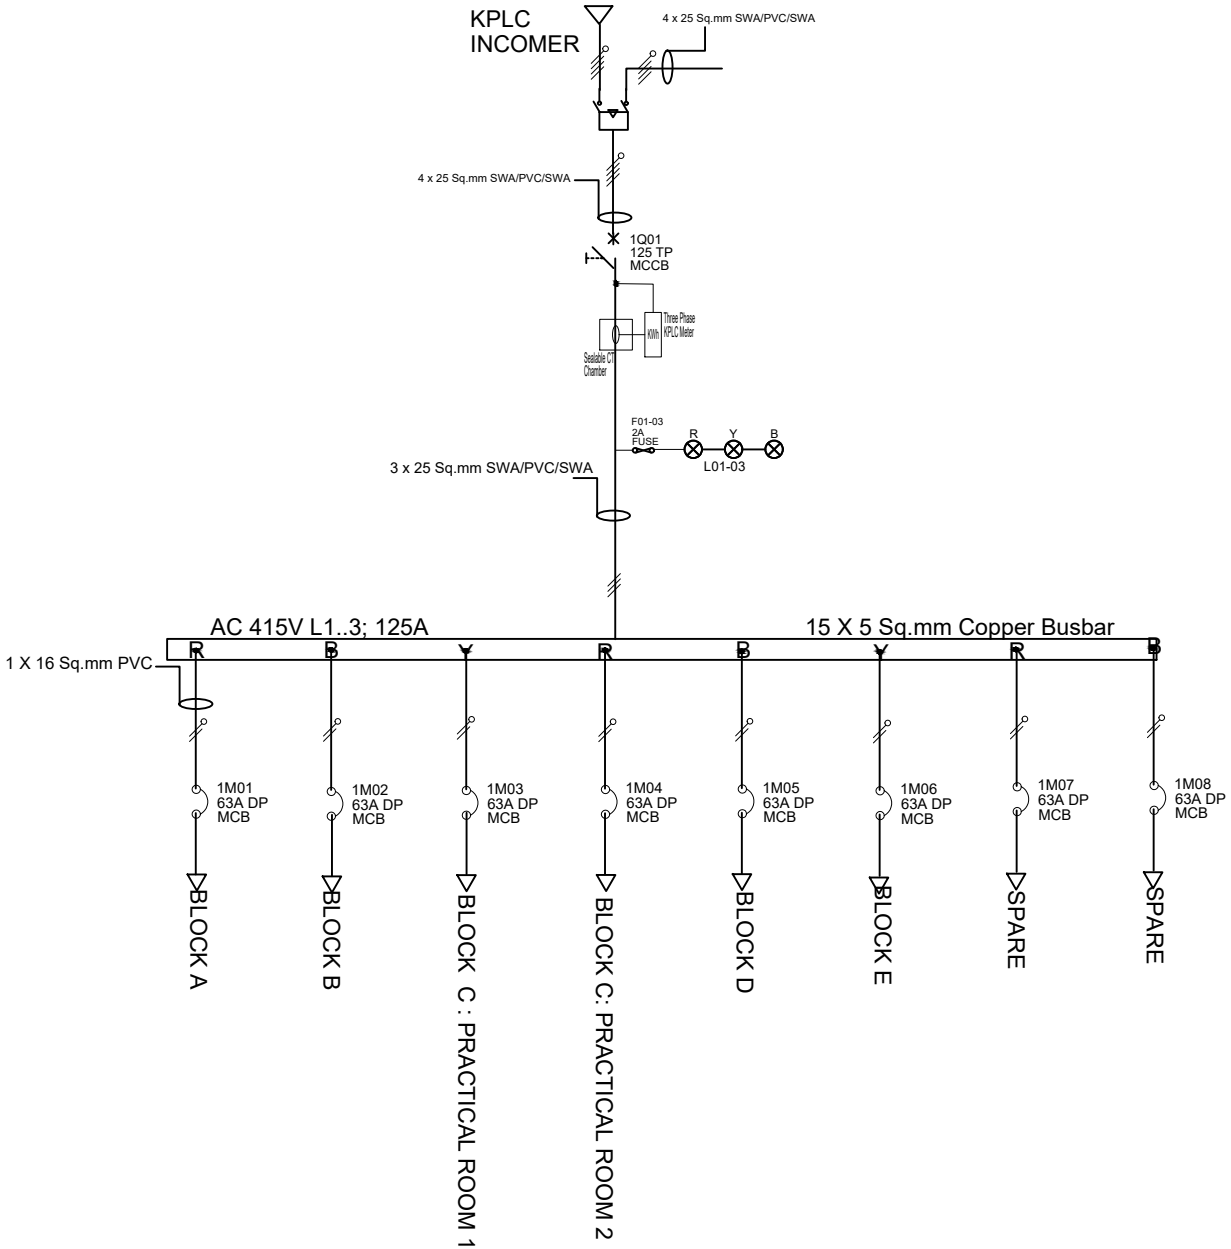

		PLEASE RETURN THE DOCUMENT WITH:		TITLE: SINGLE LINE DIAGRAM	DRAWN BY: Stu.Eng.Brian Mumo	P.S
		NAME :	STAMP:		APPROVED BY: Eng.Vincent..Jumba	A4
R1	25/2/2026	SIGNATURE :		PROJECT: HADU VOCATIONAL TRAINIG CENTRE	DATE: 25/2/2026	Sh.No: 1
R0	19/2/2026	DATE :		CLIENT: ARCHSAN ASSOCIATES	QUOTE REF:Q001	Drg.No: 1

THIS DOCUMENT IS PROPERTY OF KESLTD. & DUPLICATION OF ANY KIND IS PROHIBITED

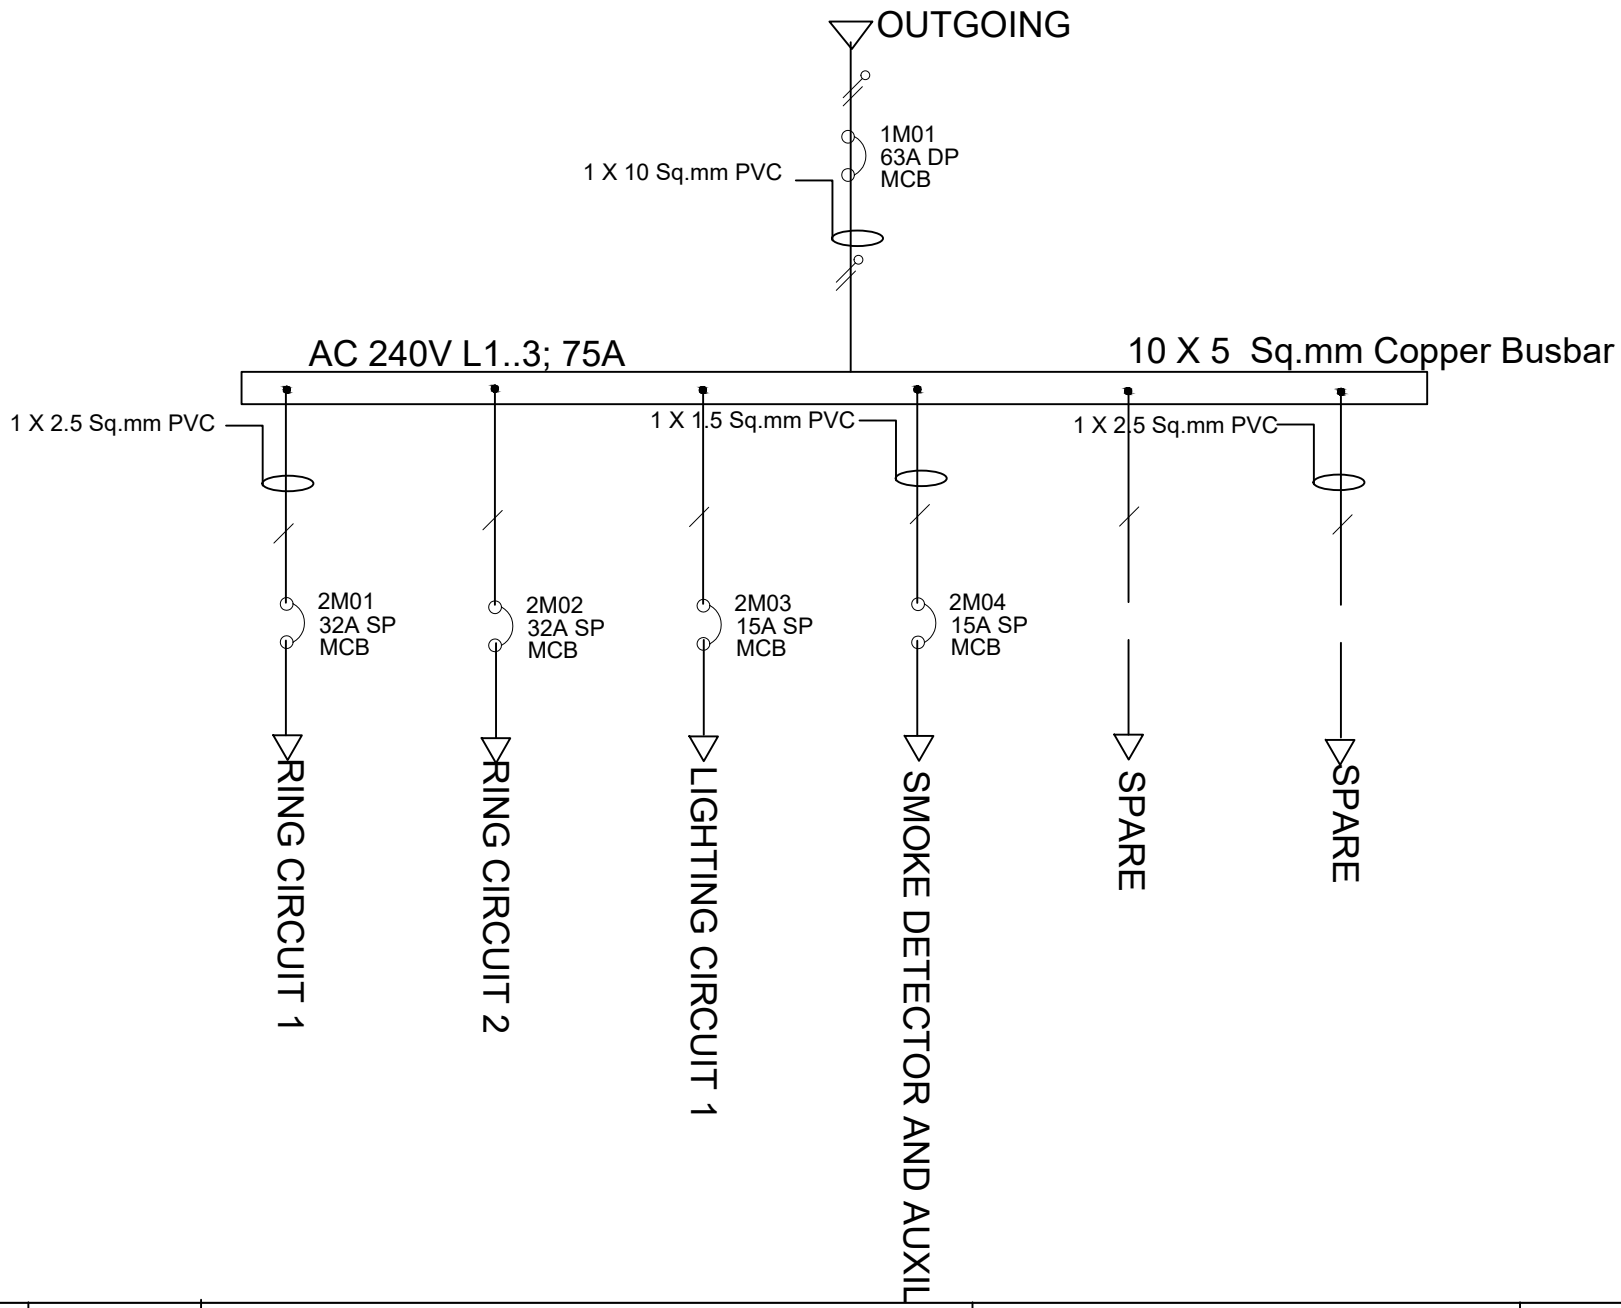

		PLEASE RETURN THE DOCUMENT WITH:		TITLE: 6 WAY CONSUMER CCU SLD	DRAWN BY: Stu.Eng.Brian Mumo	P.S
		NAME :	STAMP:		APPROVED BY: Eng.Vincent..Jumba	A4
R1	25/2/2026	SIGNATURE :		PROJECT: HADU VOCATIONAL TRAINIG CENTRE	DATE: 25/2/2026	Sh.No: 1
R0	19/2/2026	DATE :		CLIENT: ARCHSAN ASSOCIATES	QUOTE REF:Q001	Drg.No: 1